
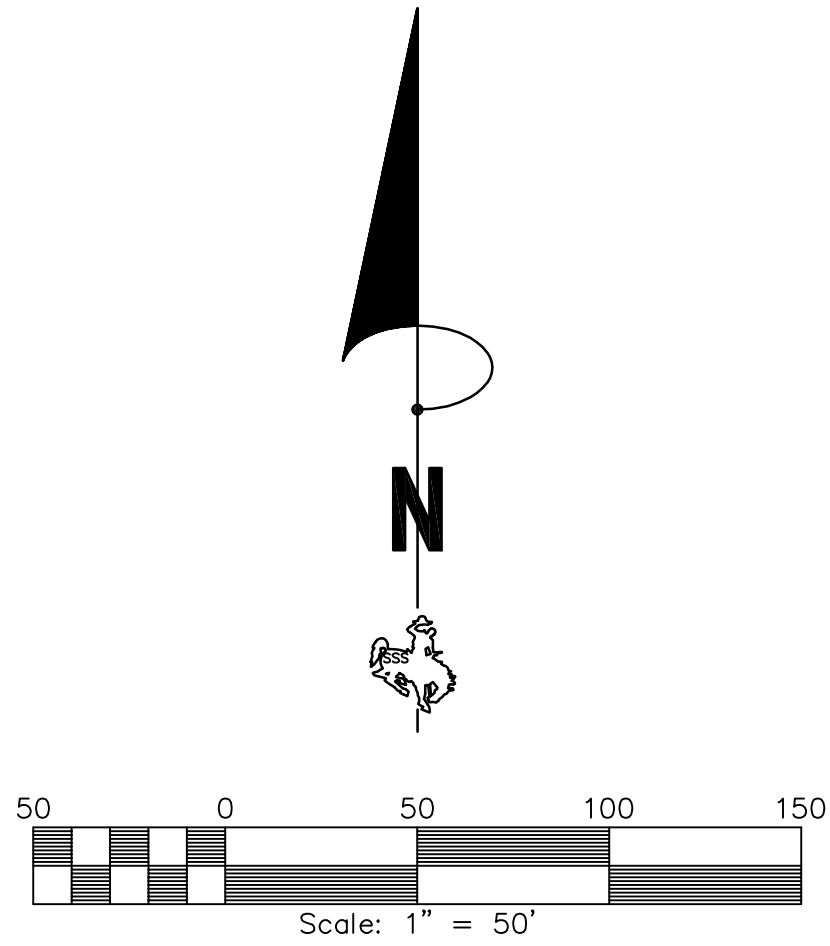


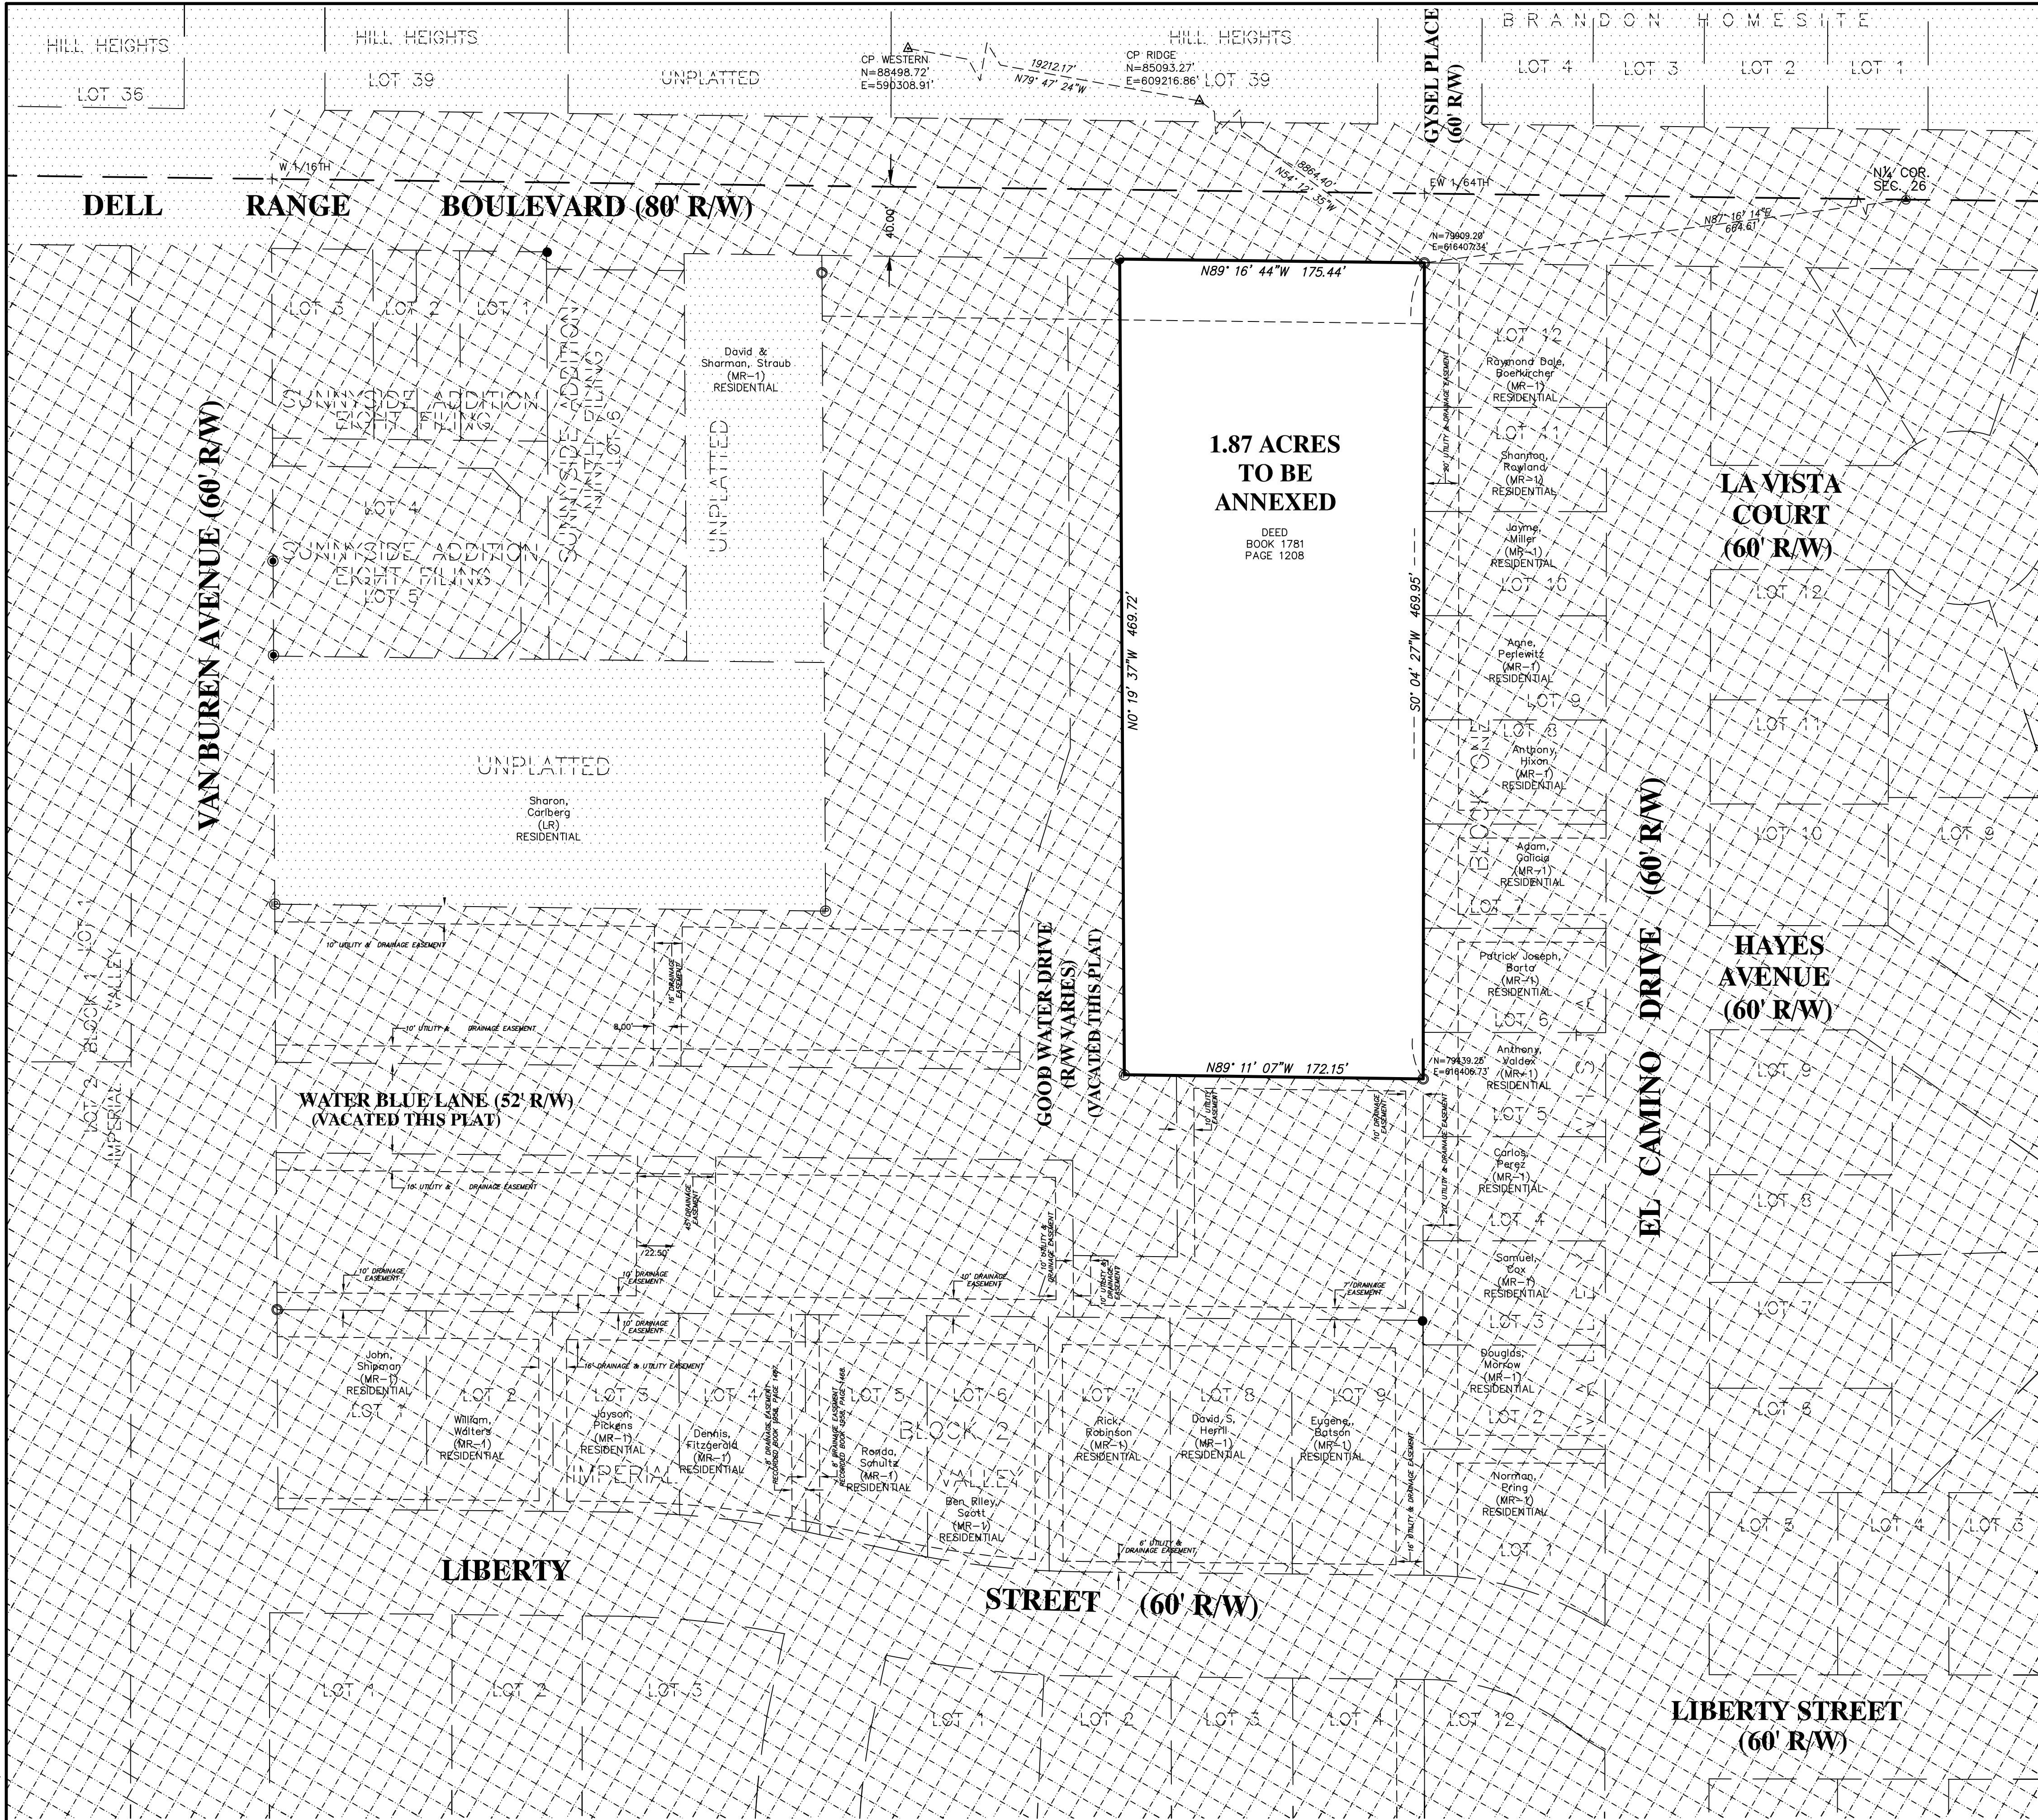

- LEGEND**
- FOUND 1½" ALUMINUM CAP STAMPED "SSS P.L.S. 2500"
 - SET ¾" x 24" LONG REBAR WITH 1½" ALUMINUM CAP STAMPED "SSS P.L.S. 5910"
 - ▲ FOUND 3 ½" ALUMINUM CAP MARKED "PLS 2500"
 - FOUND 1½" ALUMINUM CAP ILLEGIBLE
 - ⊙ FOUND 1½" ALUMINUM CAP STAMPED "PLS 9843"
 - ⊙ FOUND ½" IRON PIPE
 - ▨ LANDS CURRENTLY INCORPORATED WITHIN THE CITY OF CHEYENNE CORPORATE LIMITS
 - ▤ OTHER LANDS CURRENTLY OUTSIDE OF THE CITY OF CHEYENNE CORPORATE LIMITS (COUNTY)
 - AREA TO BE ANNEXED

NOTES

- 1) BASIS OF AZIMUTH — CITY OF CHEYENNE DATUM REFERENCED FROM CITY CONTROL MONUMENTS "CP COLLEGE" & "CP EAST".
- 2) NO PORTION OF THE SUBJECT PROPERTY FALLS WITHIN FEMA SPECIAL 100-YEAR FLOOD HAZARD AREA AS SHOWN ON F.I.R.M. PANEL # 56021C1091F, DATED JANUARY 17, 2007.
- 3) WATER AND SEWER TO BE PROVIDED BY CITY OF CHEYENNE BOPU.
- 4) ALL UTILITIES TO BE PROVIDED IN ADJACENT RIGHT-OF-WAY.
- 5) NEAREST FIRE HYDRANT APPROXIMATELY 175' EAST AT THE CORNER OF LA VISTA CT.

APPROVALS

Approved by the Council of the City of Cheyenne, Wyoming this ____ day of _____, 2014.

ATTEST:
City Clerk


Mayor

CERTIFICATE OF SURVEYOR

I, Jeffrey B. Jones, Registered Professional Land Surveyor in the State of Wyoming, for and on behalf of Steil Surveying Services, LLC, hereby state, to the best of my knowledge, information and belief, that this map was prepared from field notes taken during an actual survey made by me or under my direct supervision; and that this map correctly shows the results of said survey and that the monuments found or set are as shown.

**ANNEXATION
MAP
FOR
DEL-VAN
STORAGE
PARK**

SITUATED ON A PORTION OF
THE NORTH EAST QUARTER OF THE NORTH
WEST QUARTER OF SECTION 26
T.14N. R.66W. 6TH P.M.
CITY OF CHEYENNE,
LARAMIE COUNTY, WYOMING
PREPARED May 14

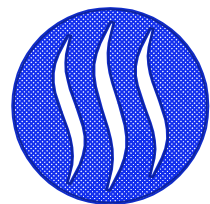

STEIL SURVEYING SERVICES, LLC
PROFESSIONAL LAND SURVEYORS

1102 WEST 19th ST. CHEYENNE, WY. 82001 • (307) 634-7273
756 GILCHRIST ST. WHEATLAND, WY. 82201 • (307) 322-9789

