
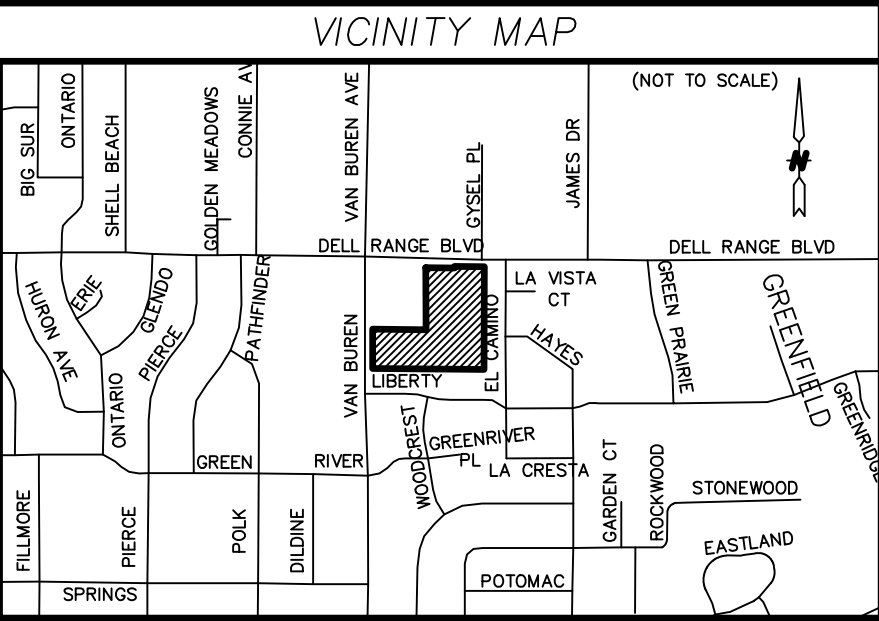
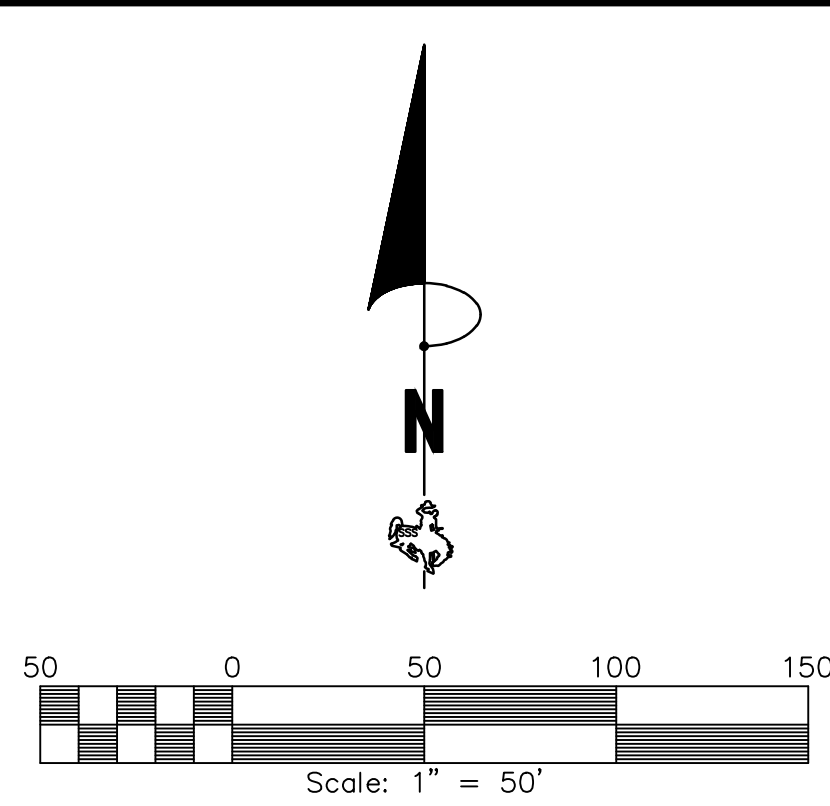


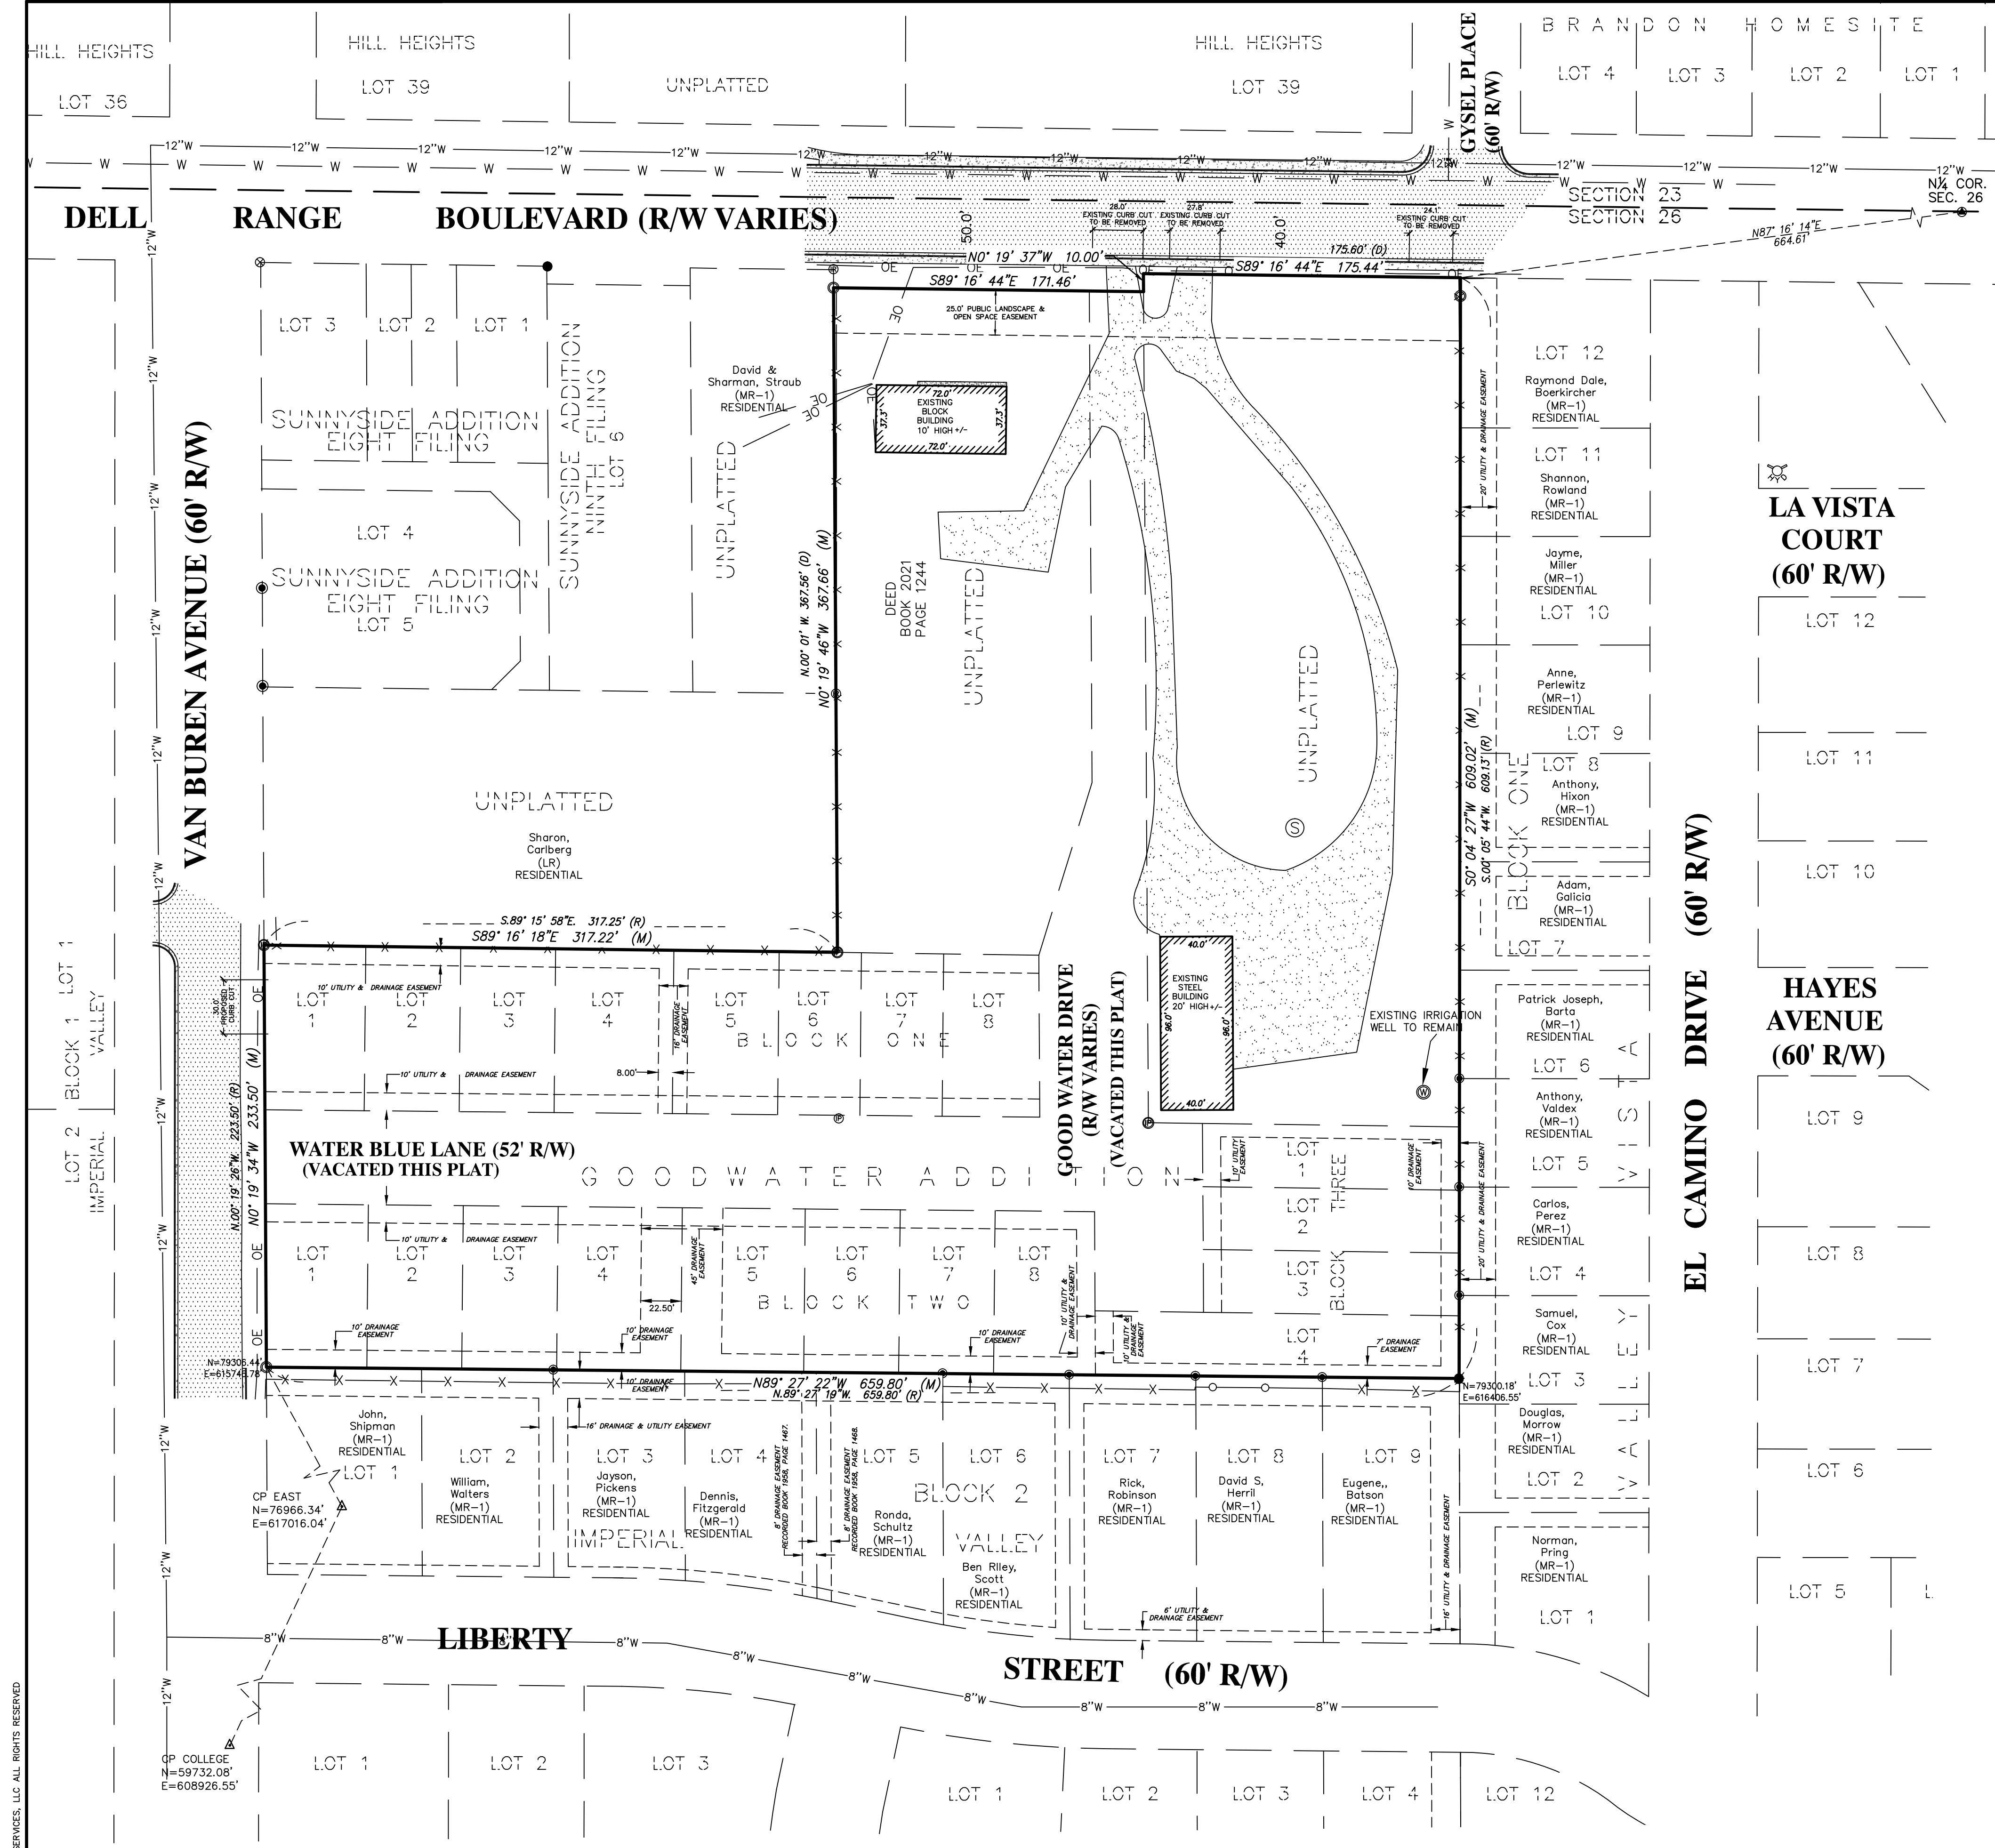

- LEGEND**
- FOUND 3/4" ALUMINUM CAP MARKED "PLS 2500"
 - FOUND 1 1/2" ALUMINUM CAP ILLEGIBLE
 - FOUND 1 1/2" ALUMINUM CAP STAMPED "PLS 9843"
 - FOUND 1/2" IRON PIPE
 - EXISTING ELECTRIC BOX
 - X SPOT ELEVATION
 - ⋈ EXISTING FIRE HYDRANT
 - ⋈ EXISTING WATER VALVE
 - EXISTING UTILITY POLE
 - ⊙ EXISTING SEPTIC
 - ⊙ EXISTING WELL
 - ⊙ EXISTING SINGLE POST SIGN
 - EXISTING GUY WIRE
 - ⊞ EXISTING TELEPHONE PEDESTAL
 - EXISTING OVERHEAD ELECTRIC LINES
 - EXISTING WATER LINE
 - SA — EXISTING SANITARY SEWER LINE
 - ▨ EXISTING BITUMINOUS SURFACE
 - ▨ EXISTING CONCRETE SURFACE
 - ▨ EXISTING GRAVEL SURFACE
- ZONING**
- EXISTING ZONING MU(COUNTY), MUB, MR-1
PROPOSED ZONING MUE(MIXED USE EMPLOYMENT DISTRICT)
- PROPOSED USE**
- MINI STORAGE

LAND DESCRIPTION

All of Goodwater Addition, City of Cheyenne and a being a portion of land in the Northeast Quarter of the Northwest Quarter (NE1/4NW1/4) of Section 26, Township 14 North Range 66 West of the 6th P.M., Laramie County, Wyoming, more particularly described as follows:


Beginning at the Northwest corner of Valley Vista Addition from which the North Quarter Corner of Section 26 bears N.87°16'14"E., a distance of 664.61 feet; thence S.00°04'27"W., along the line common to Valley Vista and Goodwater Addition, a distance of 609.02 feet, to the Southeast corner of Goodwater Addition; thence, N.89°27'22"W., along the South line of said Goodwater Addition, a distance of 659.80 feet to a point on the East right-of-way line of Van Buren Avenue; thence, N.00°19'34"W., along said right-of-way line, a distance of 233.50 feet to the Northwest corner of Goodwater Addition; thence S.89°16'18"E., along the North line of Goodwater Addition, a distance of 317.22 feet to the Southwest corner of that Warranty Deed recorded at the Laramie County Clerks Office in Deed Book 2021, Page 1244; thence, N.00°19'46"W., along said Deed Book and Page, a distance of 367.66 feet to a point in the South right-of-way line of Dell Range Boulevard; thence S.89°16'44"E., along said right-of-way line, a distance of 171.46 feet; thence N.00°19'37"W., along said right-of-way line, a distance of 10.00 feet; thence S.89°16'44"E., along said right-of-way line, a distance of 175.44 feet to the Point of Beginning.

Containing 6.48 Acres more or less.

- NOTES**
- 1) BASIS OF AZIMUTH - CITY OF CHEYENNE DATUM REFERENCED FROM CITY CONTROL MONUMENTS "CP COLLEGE" & "CP EAST".
 - 2) NO PORTION OF THE SUBJECT PROPERTY FALLS WITHIN FEMA SPECIAL 100-YEAR FLOOD HAZARD AREA AS SHOWN ON F.I.R.M. PANEL # 56021C1091F; DATED JANUARY 17, 2007.
 - 3) WATER AND SEWER TO BE PROVIDED BY CITY OF CHEYENNE BOPU.
 - 4) ALL UTILITIES TO BE PROVIDED IN ADJACENT RIGHT-OF-WAY.
 - 5) NEAREST FIRE HYDRANT APPROXIMATELY 175' EAST AT THE CORNER OF LA VISTA CT.
- CERTIFICATE OF SURVEYOR**
- I, Jeffrey B. Jones, Registered Professional Land Surveyor in the State of Wyoming, for and on behalf of Stiel Surveying Services, LLC, hereby state, to the best of my knowledge, information and belief, that this map was prepared from field notes taken during an actual survey made by me or under my direct supervision; and that this map correctly shows the results of said survey and that the monuments found or set are as shown.

**ZONE CHANGE MAP
FOR
DEL-VAN
STORAGE
PARK**

SITUATED ON A PORTION OF
THE NE1/4 NW1/4 OF SECTION 26
T.14N. R.66W. 6TH P.M. INCLUDING ALL OF
GOODWATER ADDITION, GOODWATER DRIVE
AND WATER BLUE LANE
CITY OF CHEYENNE,
LARAMIE COUNTY, WYOMING
PREPARED May 14

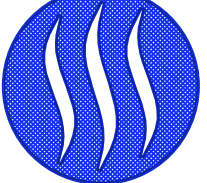

**STIEL SURVEYING SERVICES, LLC
PROFESSIONAL LAND SURVEYORS**

1102 WEST 19th ST. CHEYENNE, WY. 82001 • (307) 634-7273
756 GILCHRIST ST. WHEATLAND, WY. 82201 • (307) 322-9799