
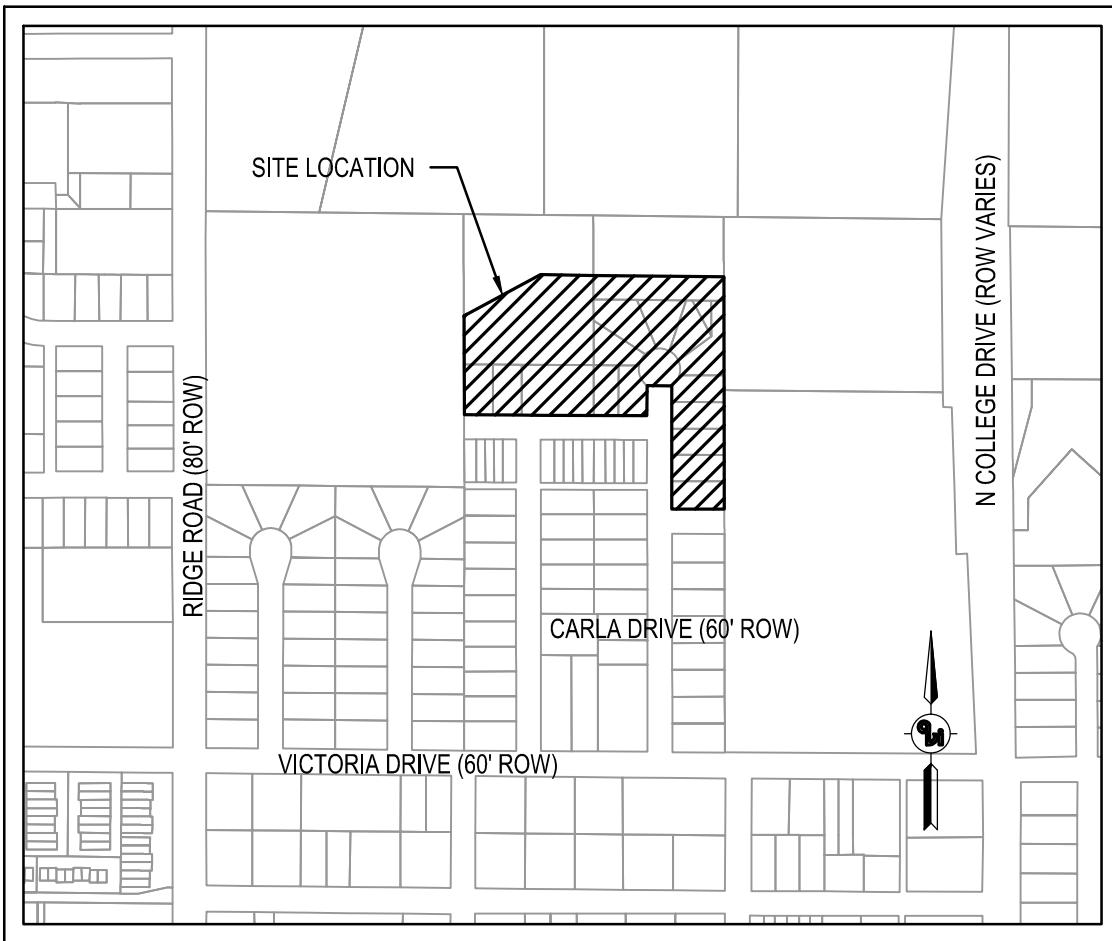


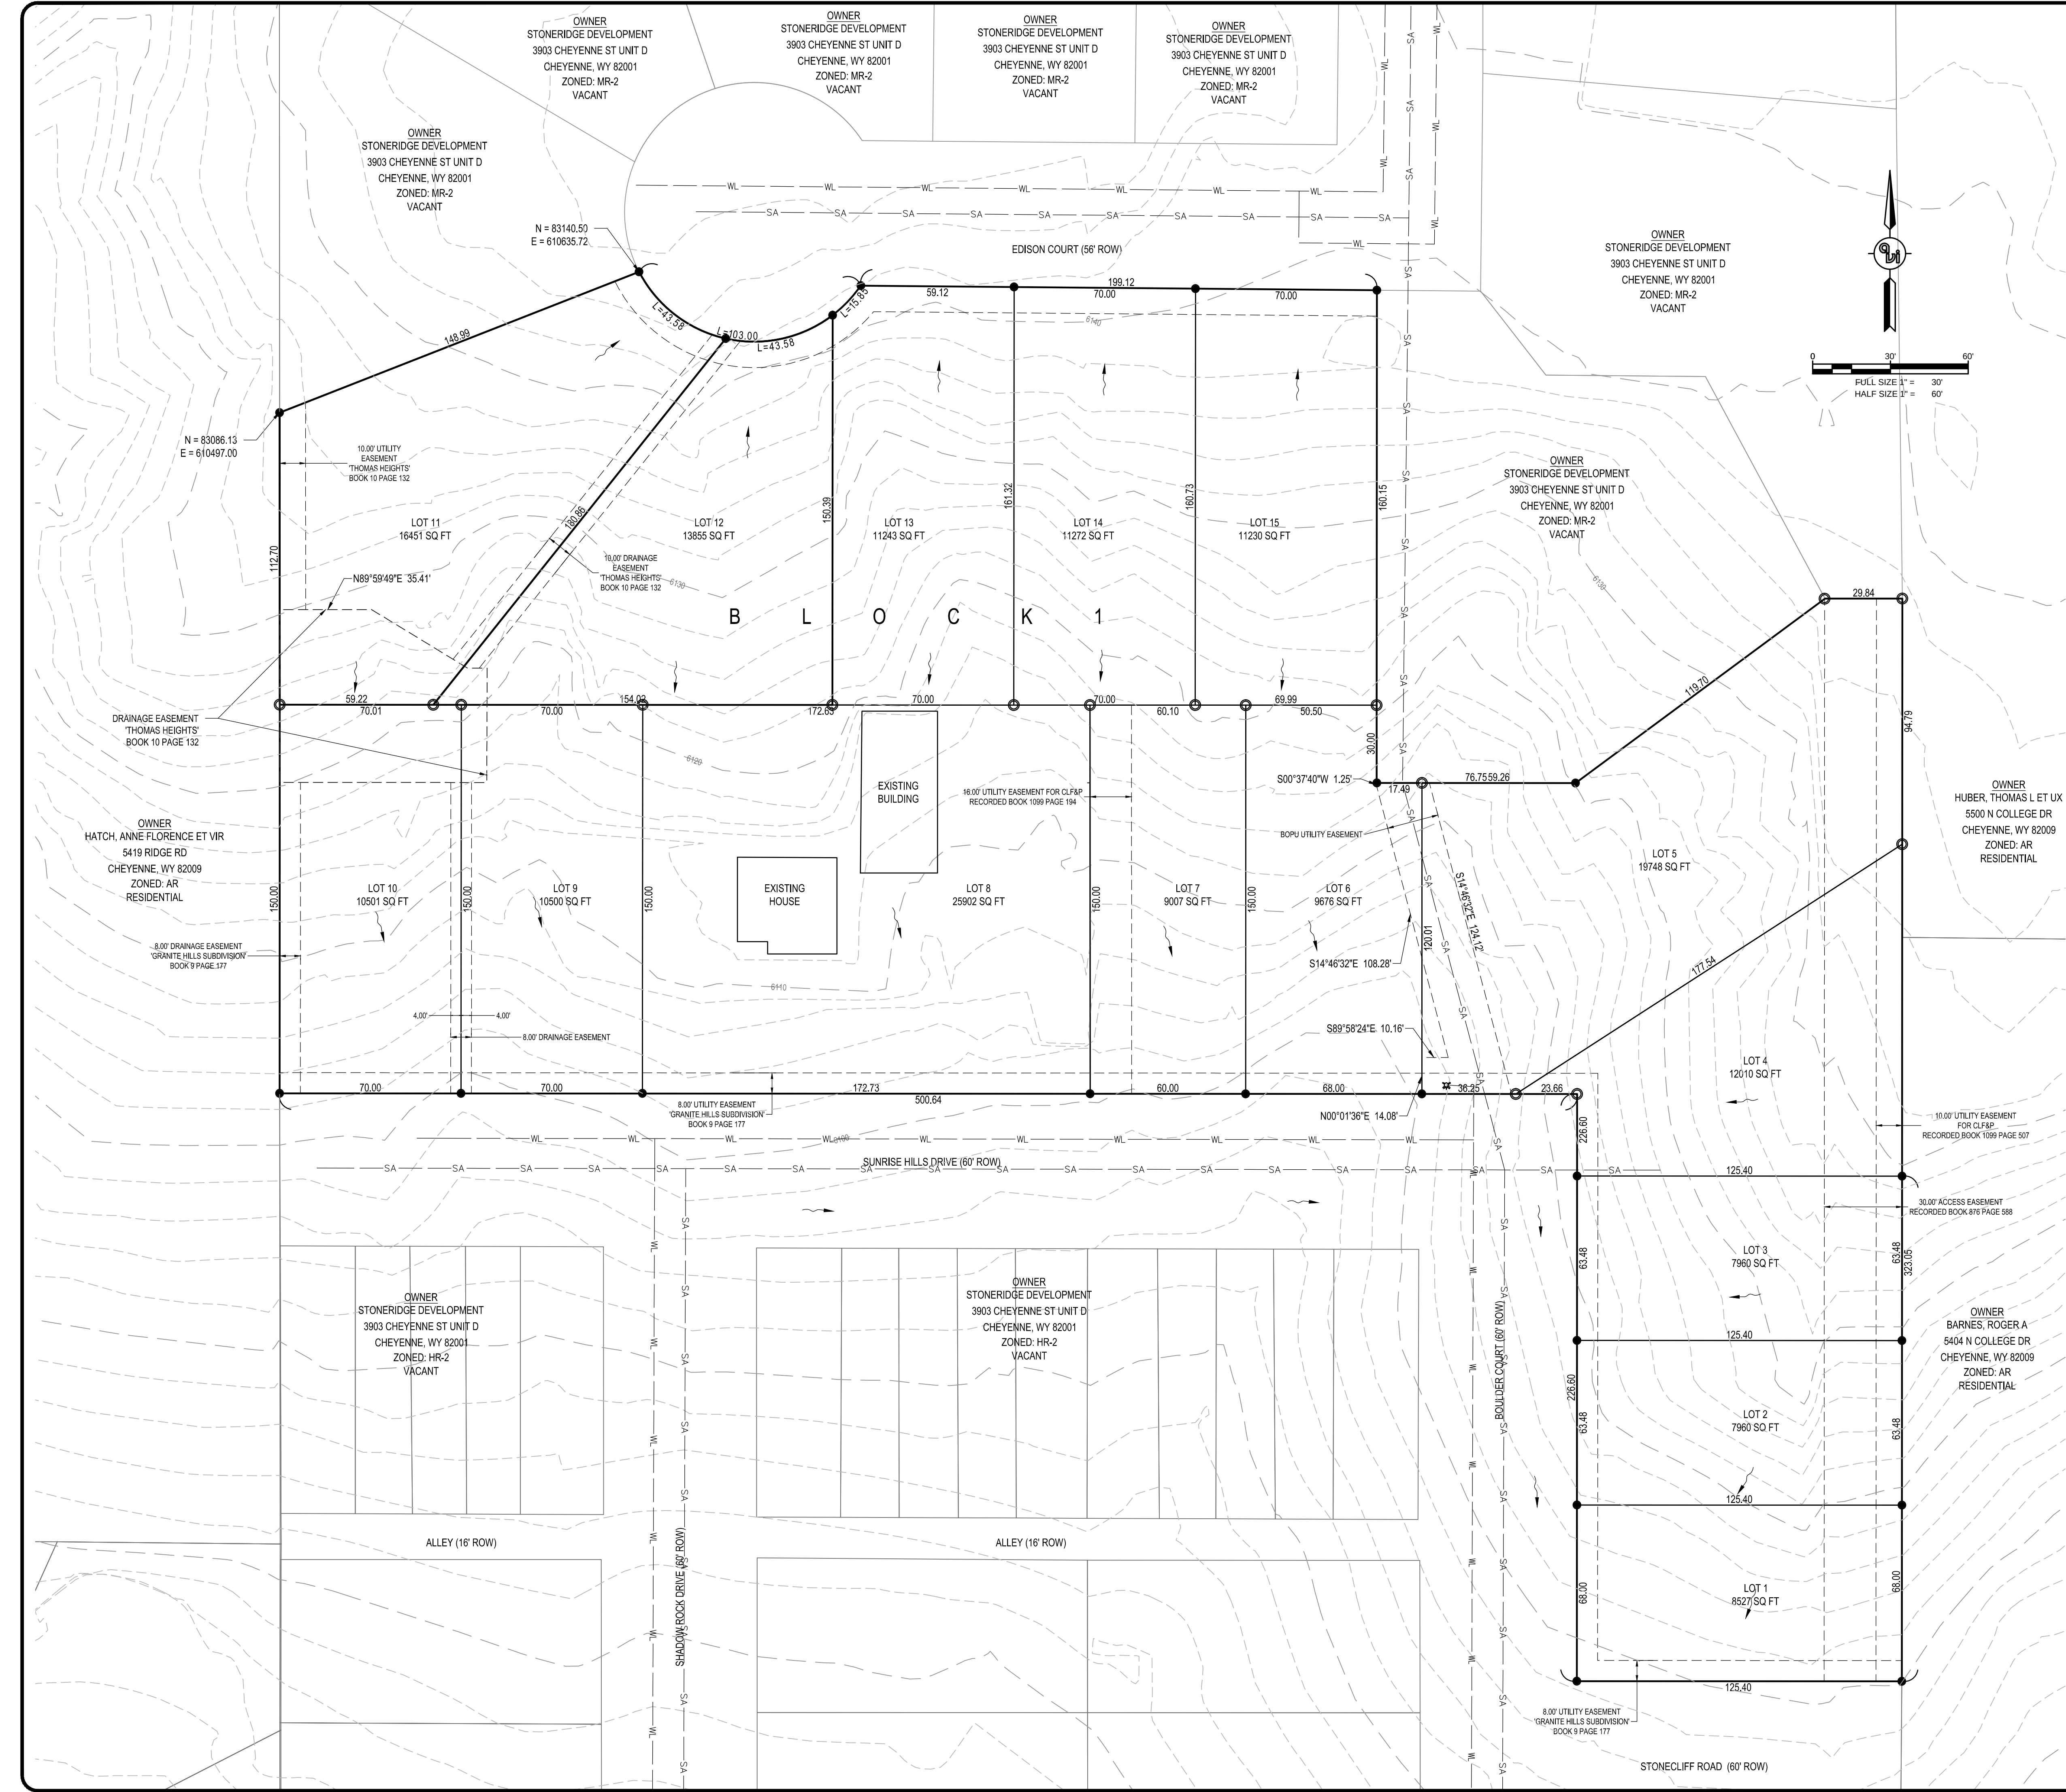

- LEGEND**
- WL DENOTES PROPOSED WATER MAINS
 - SA DENOTES PROPOSED SANITARY SEWER MAINS
 - - - - - DENOTES INTERMEDIATE CONTOUR (2' INTERVAL)
 - - - - - DENOTES INDEX CONTOUR (10' INTERVAL)
 - ↗ DENOTES DIRECTION OF SURFACE DRAINAGE
 - DENOTED FOUND ALUMINUM CAP
 - DENOTED SET ALUMINUM CAP

- NOTES:**
- PARCEL CONTAINS 4.27 ACRES ±
 - TOTAL LOTS = 14 (TOTAL RESIDENTIAL LOTS = 14)
 - TOPOGRAPHY IS FROM 2014 AERIAL MAPPING OF THE CITY AND COUNTY.
 - THERE ARE NO SPECIAL FLOOD HAZARD AREAS SHOWN ON THE FLOOD INSURANCE RATE MAPS FOR LARAMIE COUNTY PANELS 1092 OF 1650, MAP NUMBER 56021C1092F HAVING AN EFFECTIVE DATE OF JANUARY 2007
 - PROPOSED SITE IS IN FIRE DISTRICT #1
 - DOMESTIC WATER TO BE SUPPLIED BY THE CITY OF CHEYENNE
 - SANITARY SEWER SERVICE IS TO BE SUPPLIED BY THE CITY OF CHEYENNE
 - CURRENT ZONING: MR-2
 - PROPOSED ZONING: MR-2

**PRELIMINARY PLAT
OF
THOMAS HILLS**

A REPLAT OF LOTS 1-5 AND LOTS 10-15 BLOCK 3 OF 'GRANITE HILLS SUBDIVISION' AND LOTS 33-37 BLOCK 8 OF 'THOMAS HEIGHTS', ALSO BEING SITUATED IN A PORTION OF THE SE1/4 NW1/4 AND THE NE1/4 SW1/4 OF SECTION 22, TOWNSHIP 14 NORTH, RANGE 66 WEST OF THE 6TH PRINCIPAL MERIDIAN, CHEYENNE, WYOMING.
PREPARED JULY 2015

DATE	
REVISION	
NO.	
PREPARED FOR: STONERIDGE DEVELOPMENT 3903 CHEYENNE ST UNIT D CHEYENNE, WY 82001	
PROJECT: THOMAS HILLS	
DRAWING TITLE: PRELIMINARY PLAT	
307.637.6017 1103 OLD TOWN LANE, SUITE 101 CHEYENNE, WY 82009 AVI@AVIPC.COM	
DATE:	JULY 2015
DRAWN BY:	MLB
DESIGNED BY:	
CHECKED BY:	AED
JOB NO.:	3701
DRAWING NO.	1 OF 1