
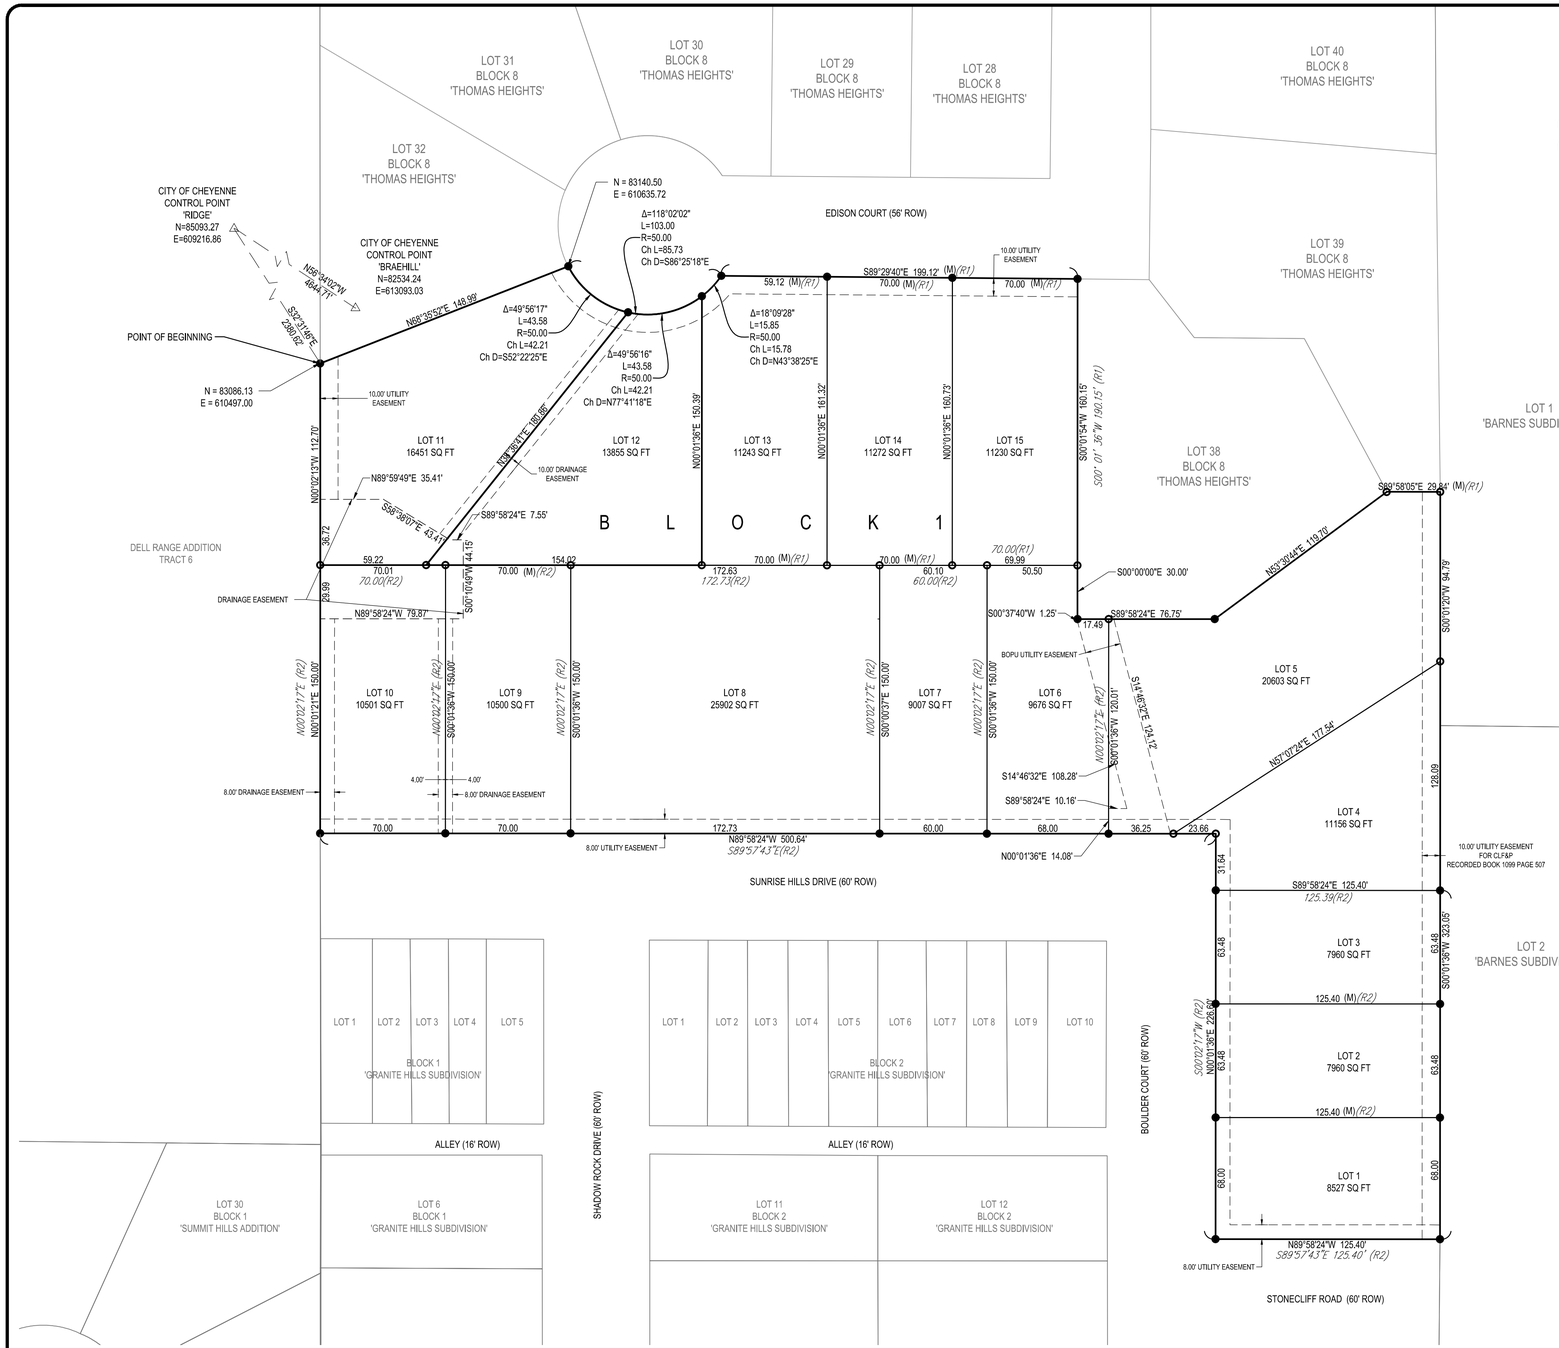


LEGEND:

- ● FOUND ALUMINUM CAP
- ○ SET ALUMINUM CAP
- (M) MEASURED DATA THIS PLAT
- (R1) RECORDED DATA FROM 'THOMAS HEIGHTS'
- (R2) RECORDED DATA FROM 'GRANITE HILLS SUBDIVISION'

0 40' 80'

FULL SIZE 1" = 40'
HALF SIZE 1" = 80'

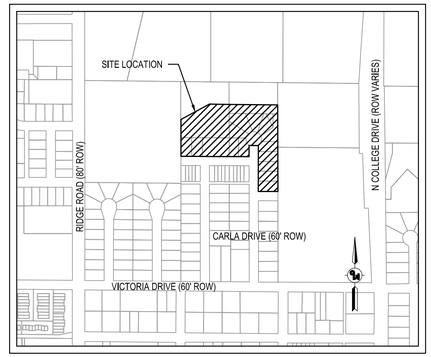

VICINITY MAP
N.T.S.

LEGAL DESCRIPTION

A REPLAT OF LOTS 1-5 AND LOTS 10-15 BLOCK 3 OF 'GRANITE HILLS SUBDIVISION' AND LOTS 33-37 BLOCK 8 OF 'THOMAS HEIGHTS', ALSO BEING SITUATED IN A PORTION OF THE SE1/4 NW1/4 AND THE NE1/4 SW1/4 OF SECTION 22, TOWNSHIP 14 NORTH, RANGE 66 WEST OF THE 6TH PRINCIPAL MERIDIAN, CHEYENNE, WYOMING AND BEING MORE PARTICULARLY DESCRIBED BY METES AND BOUNDS AS FOLLOWS:

BEGINNING AT THE SOUTHWEST CORNER OF LOT 32 BLOCK 8 OF THOMAS HEIGHTS; THENCE N68°35'52"E A DISTANCE OF 148.99 FEET TO THE BEGINNING OF A CURVE CONCAVE TO THE NORTH, SAID CURVE HAVING A RADIUS OF 50.00 FEET, A CENTRAL ANGLE OF 118°02'02", A CHORD BEARING OF S86°25'18"E AT A DISTANCE OF 85.73 FEET, THENCE ALONG THE ARC OF SAID CURVE 103.00 FEET TO A POINT; THENCE S89°29'40"E A DISTANCE OF 199.12 FEET TO A POINT; THENCE S00°01'54"W A DISTANCE OF 160.15 FEET TO A POINT; THENCE S00°00'00"E A DISTANCE OF 30.00 FEET TO A POINT; THENCE S89°58'24"E A DISTANCE OF 76.75 FEET TO A POINT; THENCE N53°30'44"E A DISTANCE OF 119.70' TO A POINT; THENCE S89°58'05"E A DISTANCE OF 29.84 FEET TO A POINT; THENCE S00°01'20"W A DISTANCE OF 94.79 FEET TO A POINT; THENCE S00°01'36"W A DISTANCE OF 323.05 FEET TO A POINT; THENCE N89°58'24"W A DISTANCE OF 125.40 FEET TO A POINT ON THE EAST RIGHT OF WAY LINE OF BOULDER COURT; THENCE CONTINUING ALONG THE EAST RIGHT OF WAY LINE OF SAID BOULDER COURT N00°01'36"E A DISTANCE OF 226.60 FEET TO A POINT TO THE NORTH RIGHT OF WAY LINE OF SUNRISE HILLS DRIVE; THENCE CONTINUING ALONG THE NORTH RIGHT OF WAY LINE OF SAID SUNRISE HILLS DRIVE N89°58'24"W A DISTANCE OF 500.64 FEET TO A POINT; THENCE N00°01'21"E A DISTANCE OF 150.00 FEET TO A POINT; THENCE N00°02'13"W A DISTANCE OF 112.70 FEET TO A POINT AND THE POINT OF BEGINNING.

SAID PARCEL OF LAND CONTAINS 4.27 ACRES MORE OR LESS.

VACATION STATEMENT:

THIS PLAT VACATED ANY AND ALL EXISTING LOT AND BLOCK LINES, STREETS, RIGHT OF WAYS, AND EASEMENTS WITHIN THE BOUNDS OF THIS PLAT WITH THE EXCEPTION THOSE EASEMENTS RECORDED AT THE LARAMIE COUNTY CLERKS AND RECORDER IN BOOK 1099 PAGE 507.

BASIS OF BEARINGS:

BASIS OF BEARINGS - GRID BEARINGS AS ESTABLISHED BY GPS (GLOBAL POSITIONING SYSTEM) OBSERVATIONS REFERENCED FROM CITY OF CHEYENNE CONTROL MONUMENTS "RIDGE" AND "BRAEHILL".

CERTIFICATE OF SURVEYOR

I, ADAM E DESCHLER, A PROFESSIONAL LAND SURVEYOR REGISTERED IN THE STATE OF WYOMING DO HEREBY CERTIFY THAT THIS PLAT WAS PREPARED FROM THE RECORDS AND FIELD NOTES OF A SURVEY CONDUCTED BY ME OR UNDER MY DIRECT SUPERVISION AND THAT ALL DIMENSIONS AND OTHER DETAILS ARE CORRECT TO THE BEST OF MY KNOWLEDGE AND BELIEF.

Professional Land Surveyor ADAM E. DESCHLER 12045 Date WYOMING

DEDICATION

KNOW ALL MEN BY THESE PRESENTS: THAT STONERIDGE DEVELOPMENT INC., A WYOMING CORPORATION, OWNER IN FEE SIMPLE OF THE LAND EMBRACED IN THIS FINAL PLAT OF "THOMAS HILLS," DO HEREBY DECLARE THAT THE SUBDIVISION OF SAID LAND IS WITH THEIR FREE ACT AND DEED AND IN ACCORDANCE WITH THEIR DESIRES, DO HEREBY GRANT TO THE PUBLIC THE RIGHTS OF WAY SHOWN HEREON AND GRANT THE EASEMENTS SHOWN HEREON FOR THE PURPOSES INDICATED ON THIS PLAT.

DAN MONTGOMERY, PRESIDENT OF STONERIDGE DEVELOPMENT INC

ACKNOWLEDGEMENTS

STATE OF _____)
)SS
COUNTY OF _____)

THE FOREGOING INSTRUMENT WAS ACKNOWLEDGED BEFORE ME BY DAN MONTGOMERY, PRESIDENT OF STONERIDGE DEVELOPMENT INC., A WYOMING CORPORATION, THIS ___ DAY OF _____, 2015, WITNESS MY HAND AND OFFICIAL SEAL.

NOTARY PUBLIC, _____, WYOMING

MY COMMISSION EXPIRES_____

APPROVALS

APPROVED BY THE CHEYENNE PLANNING COMMISSION THIS____ DAY OF_____, 2015.

DEVELOPMENT DIRECTOR

APPROVED BY THE CITY COUNCIL OF THE CITY OF CHEYENNE, THIS ____ DAY OF _____, 2015.

_____ _____
MAYOR CITY CLERK

FILING RECORD

FINAL PLAT
OF
THOMAS HILLS

A REPLAT OF LOTS 1-5 AND LOTS 10-15 BLOCK 3 OF 'GRANITE HILLS SUBDIVISION' AND LOTS 33-37 BLOCK 8 OF 'THOMAS HEIGHTS' , ALSO BEING SITUATED IN A PORTION OF THE SE1/4 NW1/4 AND THE NE1/4 SW1/4 OF SECTION 22, TOWNSHIP 14 NORTH, RANGE 66 WEST OF THE 6TH PRINCIPAL MERIDIAN, CHEYENNE, WYOMING.
PREPARED JULY 2015

NO.	REVISION	DATE

PREPARED FOR:
STONERIDGE DEVELOPMENT
3903 CHEYENNE ST UNIT D
CHEYENNE, WY 82001

PROJECT: THOMAS HILLS

DRAWING TITLE: FINAL PLAT

ENGINEERING PLANNING SURVEYING
307.637.6017
1103 OLD TOWN LANE, SUITE 101
CHEYENNE, WY 82009
AVI@AVIPC.COM

DATE: JULY 2015
DRAWN BY: MLB
DESIGNED BY:
CHECKED BY: AED
JOB NO.: 3701
DRAWING NO. 1 OF 1