



A COMMUNITY OF CHOICE

## Development Department

2101 O'Neil Avenue, Suite 202, Cheyenne WY 82001  
(Phone) 307-637-6282 (Fax) 307-637-6366

### MEMORANDUM

TO: Mayor Kaysen and City Council  
FROM: Development Department (Mike Tylka)  
SUBJECT: Holmes Corner Preliminary Plat - Updated Map Submission & Conditions  
Clarification (UDC-15-00816)  
DATE: February 11, 2016

---

Mayor Kaysen and City Council Members,

On Tuesday, February 2<sup>nd</sup>, the day after the Planning Commission Meeting, the agent for the Holmes Corner Preliminary Plat submitted a document that sought to address Planning Commission conditions and Staff concerns. On Thursday, February 4<sup>th</sup>, the agent and other members of the team sat down with City Staff for the first time to discuss the project. In this meeting, all parties went over staff concerns, Planning Commission Conditions, and how to move forward. The agent has addressed a number of Staff concerns.

At this time Staff seeks to clarify earlier conditions and offer revised ones. Planning Commission recommended the following:

- 1.) *A determination be made in regards to current and future proposed zoning districts that may or may not be sought at the site*
- 2.) *Right-of-way dedications be amended to reflect the Engineering Departments recommendations*
- 3.) *That BOPU, access, and drainage easements be addressed per the BOPU's and City Staffs' comments.*

Staff would like to recommend edited Conditions One and Three and the elimination of Condition Two. These read as follows:

- 1.) ***That Lots 3-5 be identified for future zoning of NR-3 Neighborhood Residential – High Density or CB Community Business.***
- 2.) ***That the Board of Public Utilities concerns are met in regards to the reuse water line running through the property.***

In addition, at the meeting on the 4<sup>th</sup> the agent stated that they would address Staff concerns regarding street network connectivity and block size standards, as of the date of this memo the agent has not, and therefore Staff is recommending a third condition as follows:

- 3.) ***That the applicant addresses street network connectivity and block size standards as identified in the Unified Development Code.***

Attached are the third set of maps submitted by the agent, dated February 3<sup>rd</sup>, 2016 that did not make it into the City Council submission. Please do not hesitate to contact the Development Department to discuss this matter further. Thank you.

| CURVE TABLE |            |          |               |              |            |
|-------------|------------|----------|---------------|--------------|------------|
| CURVE #     | DELTA      | RADIUS   | CHORD BEARING | CHORD LENGTH | ARC LENGTH |
| C1(M)       | 9° 29' 40" | 1095.93' | N85° 34' 00"E | 181.40'      | 181.81'    |
| C1(R)       |            | 1095.93' | N85° 35' 26"E | 180.85'      |            |

ST. CLAIRE SUB LOT 1 BLOCK 1

SUNNYSIDE ADDITION SECOND FILING TRACT 13

LOT 1 TAXIDERM Y ADDITION LOT 2

LOT 3

SUNNYSIDE ADDITION FIRST FILING TRACT 16

WILLIS ROAD (60' R/W)

SUNNYSIDE ADDITION SECOND FILING

POR. TRACT 17

POR. TRACT 18

POR. TRACT 19

POR. TRACT 20


MCCANN AVE. (60' R/W)

## EAST PERSHING BOULEVARD (100' R/W)

VACATED POR. OMAHA RD. ORD. 1727 REC. Bk. 938 Pg. 579

WAMPLERS HEIGHTS ADDITION SECOND FILING BLOCK 2

RIDGE ROAD (70' R/W)

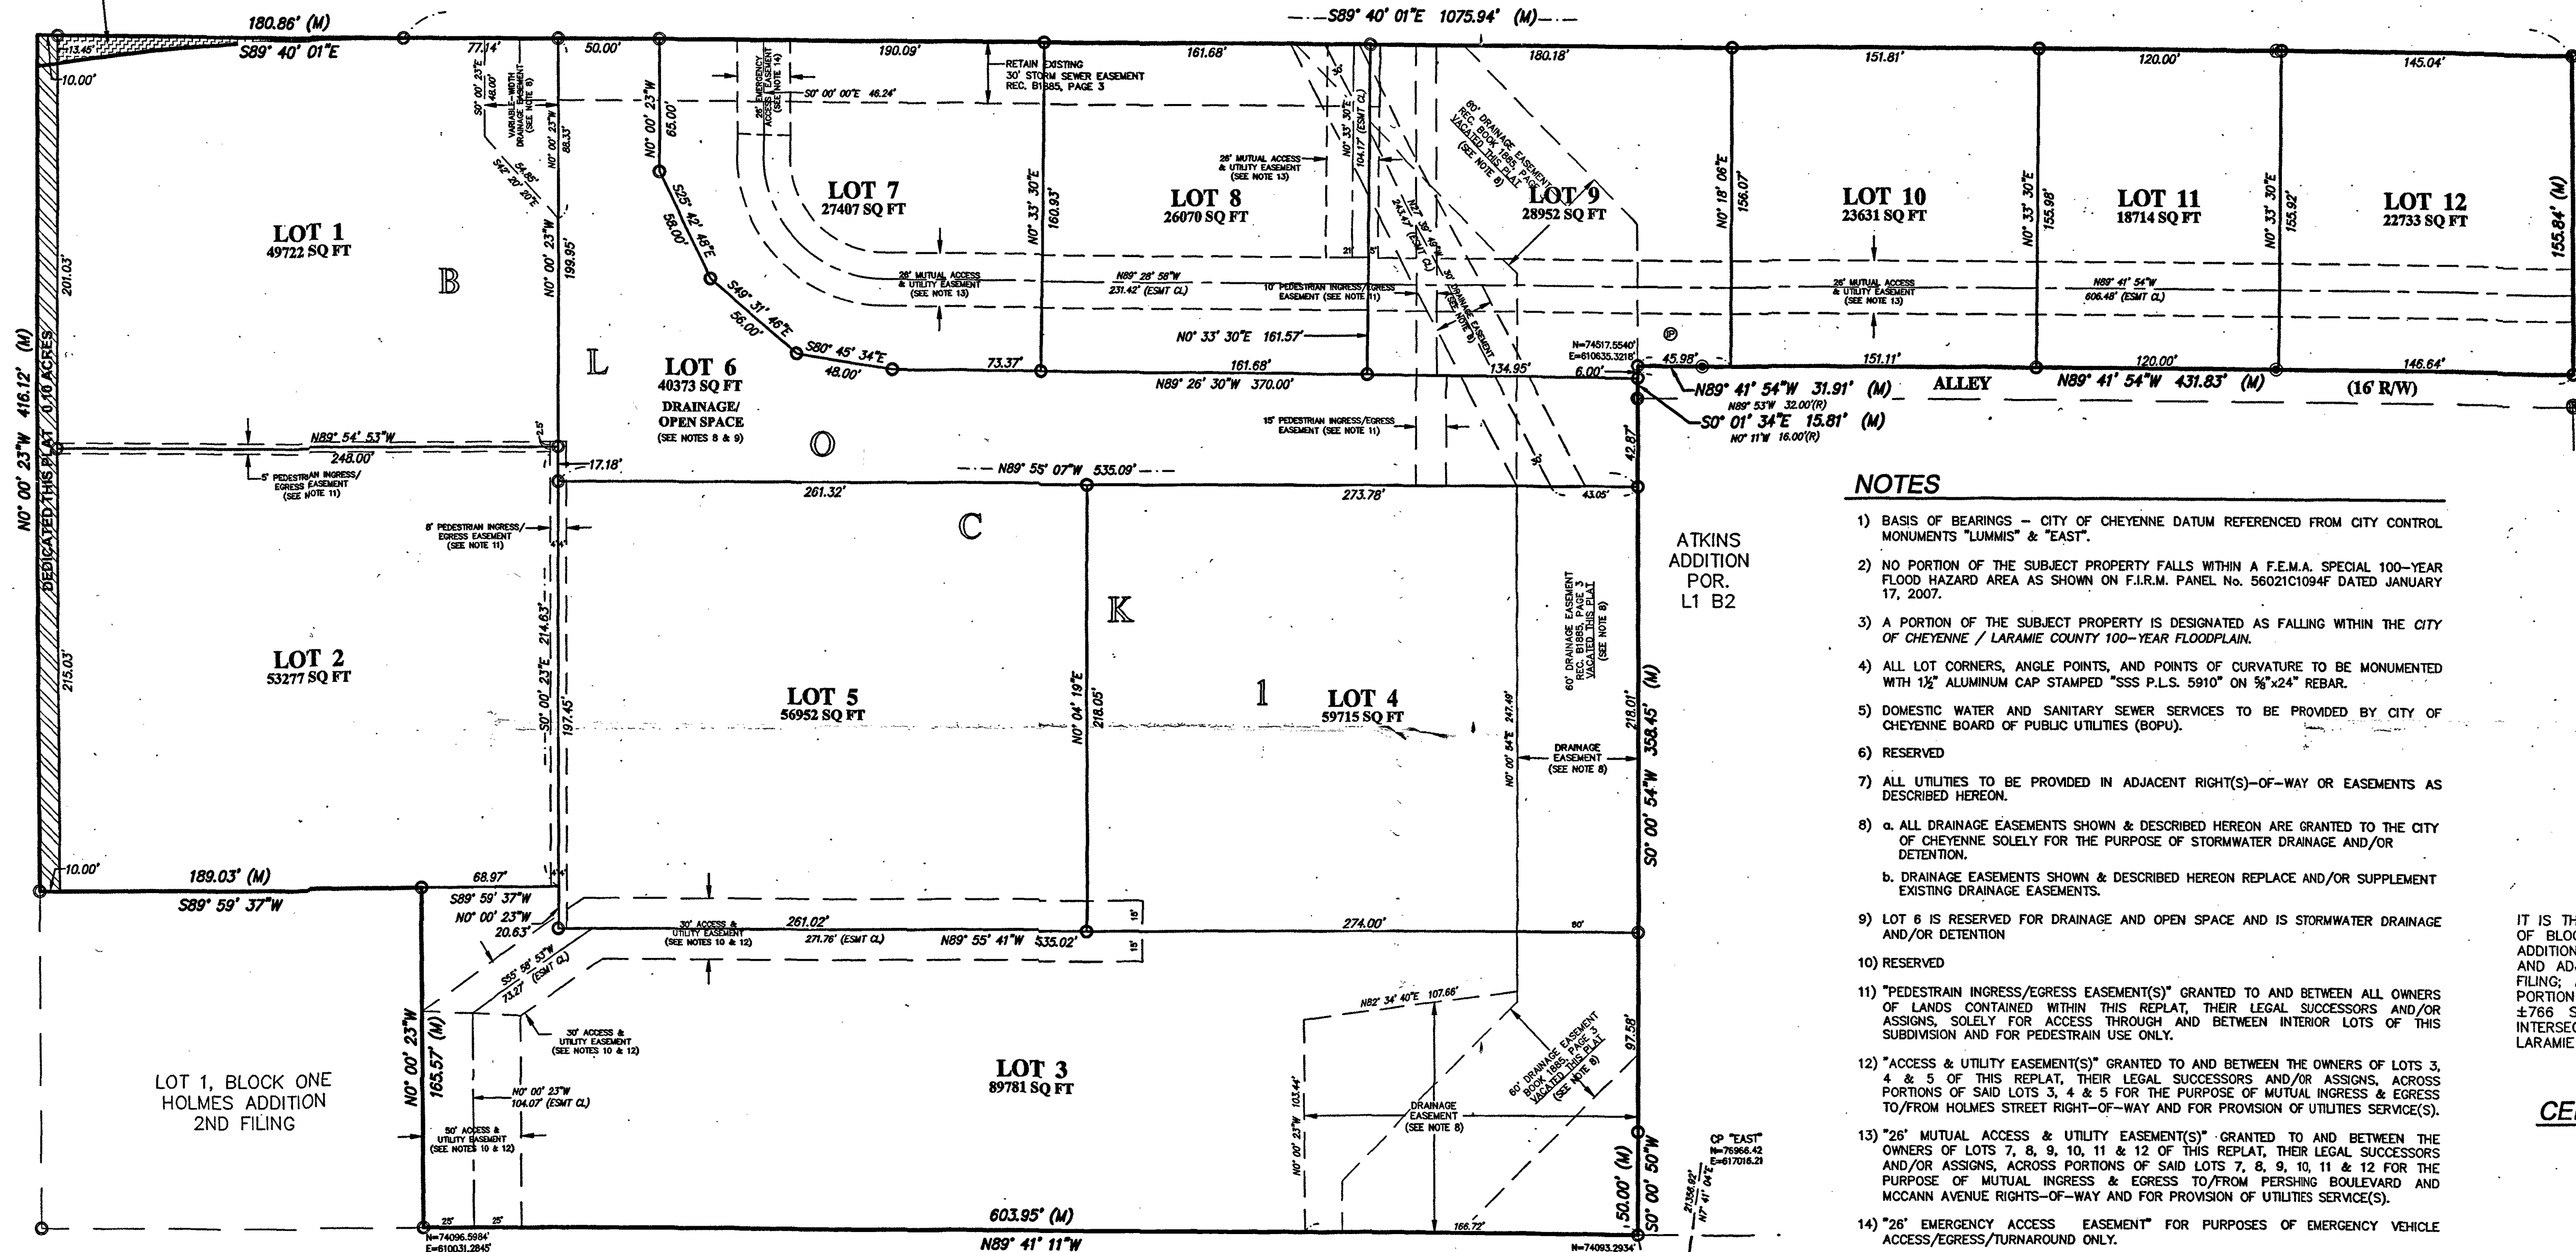

### NOTES

- 1) BASIS OF BEARINGS - CITY OF CHEYENNE DATUM REFERENCED FROM CITY CONTROL MONUMENTS "LUMMIS" & "EAST".
- 2) NO PORTION OF THE SUBJECT PROPERTY FALLS WITHIN A F.E.M.A. SPECIAL 100-YEAR FLOOD HAZARD AREA AS SHOWN ON F.I.R.M. PANEL No. 56021C1094F DATED JANUARY 17, 2007.
- 3) A PORTION OF THE SUBJECT PROPERTY IS DESIGNATED AS FALLING WITHIN THE CITY OF CHEYENNE / LARAMIE COUNTY 100-YEAR FLOODPLAIN.
- 4) ALL LOT CORNERS, ANGLE POINTS, AND POINTS OF CURVATURE TO BE MONUMENTED WITH 1/2" ALUMINUM CAP STAMPED "SSS P.L.S. 5910" ON 5/8"x24" REBAR.
- 5) DOMESTIC WATER AND SANITARY SEWER SERVICES TO BE PROVIDED BY CITY OF CHEYENNE BOARD OF PUBLIC UTILITIES (BOPU).
- 6) RESERVED
- 7) ALL UTILITIES TO BE PROVIDED IN ADJACENT RIGHT(S)-OF-WAY OR EASEMENTS AS DESCRIBED HEREON.
- 8) a. ALL DRAINAGE EASEMENTS SHOWN & DESCRIBED HEREON ARE GRANTED TO THE CITY OF CHEYENNE SOLELY FOR THE PURPOSE OF STORMWATER DRAINAGE AND/OR DETENTION.  
b. DRAINAGE EASEMENTS SHOWN & DESCRIBED HEREON REPLACE AND/OR SUPPLEMENT EXISTING DRAINAGE EASEMENTS.
- 9) LOT 6 IS RESERVED FOR DRAINAGE AND OPEN SPACE AND IS STORMWATER DRAINAGE AND/OR DETENTION
- 10) RESERVED
- 11) "PEDESTRIAN INGRESS/EGRESS EASEMENT(S)" GRANTED TO AND BETWEEN ALL OWNERS OF LANDS CONTAINED WITHIN THIS REPLAT, THEIR LEGAL SUCCESSORS AND/OR ASSIGNS, SOLELY FOR ACCESS THROUGH AND BETWEEN INTERIOR LOTS OF THIS SUBDIVISION AND FOR PEDESTRIAN USE ONLY.
- 12) "ACCESS & UTILITY EASEMENT(S)" GRANTED TO AND BETWEEN THE OWNERS OF LOTS 3, 4 & 5 OF THIS REPLAT, THEIR LEGAL SUCCESSORS AND/OR ASSIGNS, ACROSS PORTIONS OF SAID LOTS 3, 4 & 5 FOR THE PURPOSE OF MUTUAL INGRESS & EGRESS TO/FROM HOLMES STREET RIGHT-OF-WAY AND FOR PROVISION OF UTILITIES SERVICE(S).
- 13) "26" MUTUAL ACCESS & UTILITY EASEMENT(S)" GRANTED TO AND BETWEEN THE OWNERS OF LOTS 7, 8, 9, 10, 11 & 12 OF THIS REPLAT, THEIR LEGAL SUCCESSORS AND/OR ASSIGNS, ACROSS PORTIONS OF SAID LOTS 7, 8, 9, 10, 11 & 12 FOR THE PURPOSE OF MUTUAL INGRESS & EGRESS TO/FROM PERSHING BOULEVARD AND MCCANN AVENUE RIGHTS-OF-WAY AND FOR PROVISION OF UTILITIES SERVICE(S).
- 14) "26" EMERGENCY ACCESS EASEMENT" FOR PURPOSES OF EMERGENCY VEHICLE ACCESS/EGRESS/TURNAROUND ONLY.

### LEGEND

- SET "X" 24" LONG REBAR WITH 1/2" ALUMINUM CAP STAMPED "SSS P.L.S. 5910"
- FOUND 1/2" ALUMINUM CAP STAMPED "SSS P.L.S. 2500"
- FOUND 1/2" IRON PIPE
- FOUND 5/8" REBAR
- △ CITY OF CHEYENNE CONTROL MONUMENT
- (M) DENOTES MEASURED DATA THIS SURVEY
- (P) DENOTES RECORD DATA
- ▨ PUBLIC RIGHT-OF-WAY VACATED THIS PLAT (±766 SqFt)
- ▨ PUBLIC RIGHT-OF-WAY DEDICATED THIS PLAT (±4,161 SqFt)

### VACATION STATEMENT

IT IS THE INTENT OF THIS PLAT TO VACATE ALL OF THOSE REMAINING PORTIONS OF BLOCK ONE, HOLMES ADDITION, FIRST FILING; ALL OF BLOCK TWO, HOLMES ADDITION, FIRST FILING AND THAT PORTION OF VACATED WILLIS ROAD WESTERLY OF AND ADJACENT THERETO; ALL OF LOT 1, BLOCK ONE, ATKINS ADDITION, SECOND FILING; ALL OF LOT 2, BLOCK ONE, ATKINS ADDITION, SECOND FILING AND THAT PORTION OF VACATED ALLEY WESTERLY OF AND ADJACENT THERETO; AND THAT ±766 SQ. FT. PORTION OF PERSHING BOULEVARD AT THE SW CORNER OF THE INTERSECTION OF RIDGE ROAD AND PERSHING BOULEVARD; CITY OF CHEYENNE, LARAMIE COUNTY, WYOMING; INCLUDING ALL EASEMENTS AND RIGHTS-OF-WAY CONTAINED WITHIN THE PLAT BOUNDARY UNLESS SPECIFICALLY SHOWN AND DESCRIBED TO REMAIN.

### CERTIFICATE OF SURVEYOR


I, Jeffrey B. Jones, Registered Professional Land Surveyor in the State of Wyoming, for and on behalf of Steel Surveying Services, LLC, hereby state, to the best of my knowledge, information and belief, that this map was prepared from field notes taken during an actual survey made by me or under my direct supervision; and that this map correctly shows the results of said survey and that the monuments found or set are as shown.

## DRAFT FINAL PLAT OF HOLMES CORNER

A REPLAT OF ALL OF THOSE REMAINING PORTIONS OF BLOCK ONE, HOLMES ADDITION, FIRST FILING; ALL OF BLOCK TWO, HOLMES ADDITION, FIRST FILING AND THAT PORTION OF VACATED WILLIS ROAD WESTERLY OF AND ADJACENT THERETO; ALL OF LOT 1, BLOCK ONE, ATKINS ADDITION, SECOND FILING; ALL OF LOT 2, BLOCK ONE, ATKINS ADDITION, SECOND FILING AND THAT PORTION OF VACATED ALLEY WESTERLY OF AND ADJACENT THERETO; AND THAT ±766 SQ. FT. PORTION OF PERSHING BOULEVARD AT THE SW CORNER OF THE INTERSECTION OF RIDGE ROAD AND PERSHING BOULEVARD; CITY OF CHEYENNE, LARAMIE COUNTY, WYOMING


SITUATE IN THE NW¼ NW¼ OF SECTION 34, T.14N., R.66W., OF THE 6TH P.M., LARAMIE COUNTY, WYOMING

PREPARED NOVEMBER, 2015

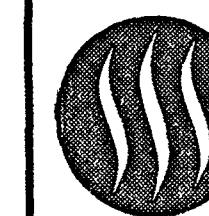


**STEEL SURVEYING SERVICES, LLC**  
PROFESSIONAL LAND SURVEYORS  
1102 WEST 19th ST. CHEYENNE, WY. 82001 • (307) 634-7273  
756 GILCHRIST ST. WHEATLAND, WY. 82201 • (307) 322-9789  
www.SteelSurvey.com • info@SteelSurvey.com

### VICINITY MAP

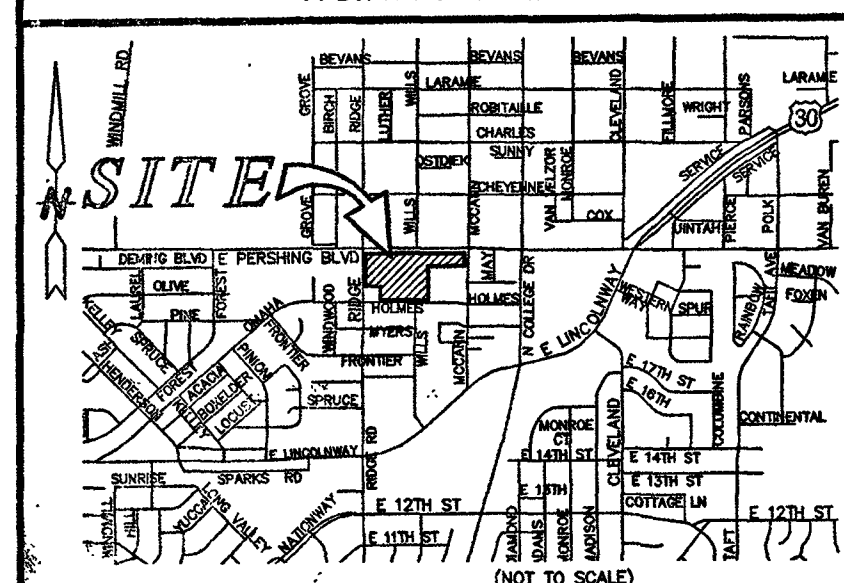

### FILING RECORD

| CURVE TABLE |            |          |               |              |
|-------------|------------|----------|---------------|--------------|
| CURVE #     | DELTA      | RADIUS   | CHORD BEARING | CHORD LENGTH |
| C1(M)       | 9° 29' 40" | 1095.93' | N85° 34' 00"E | 181.40'      |
| C1(R)       |            | 1095.93' | N85° 35.26"E  | 180.85'      |

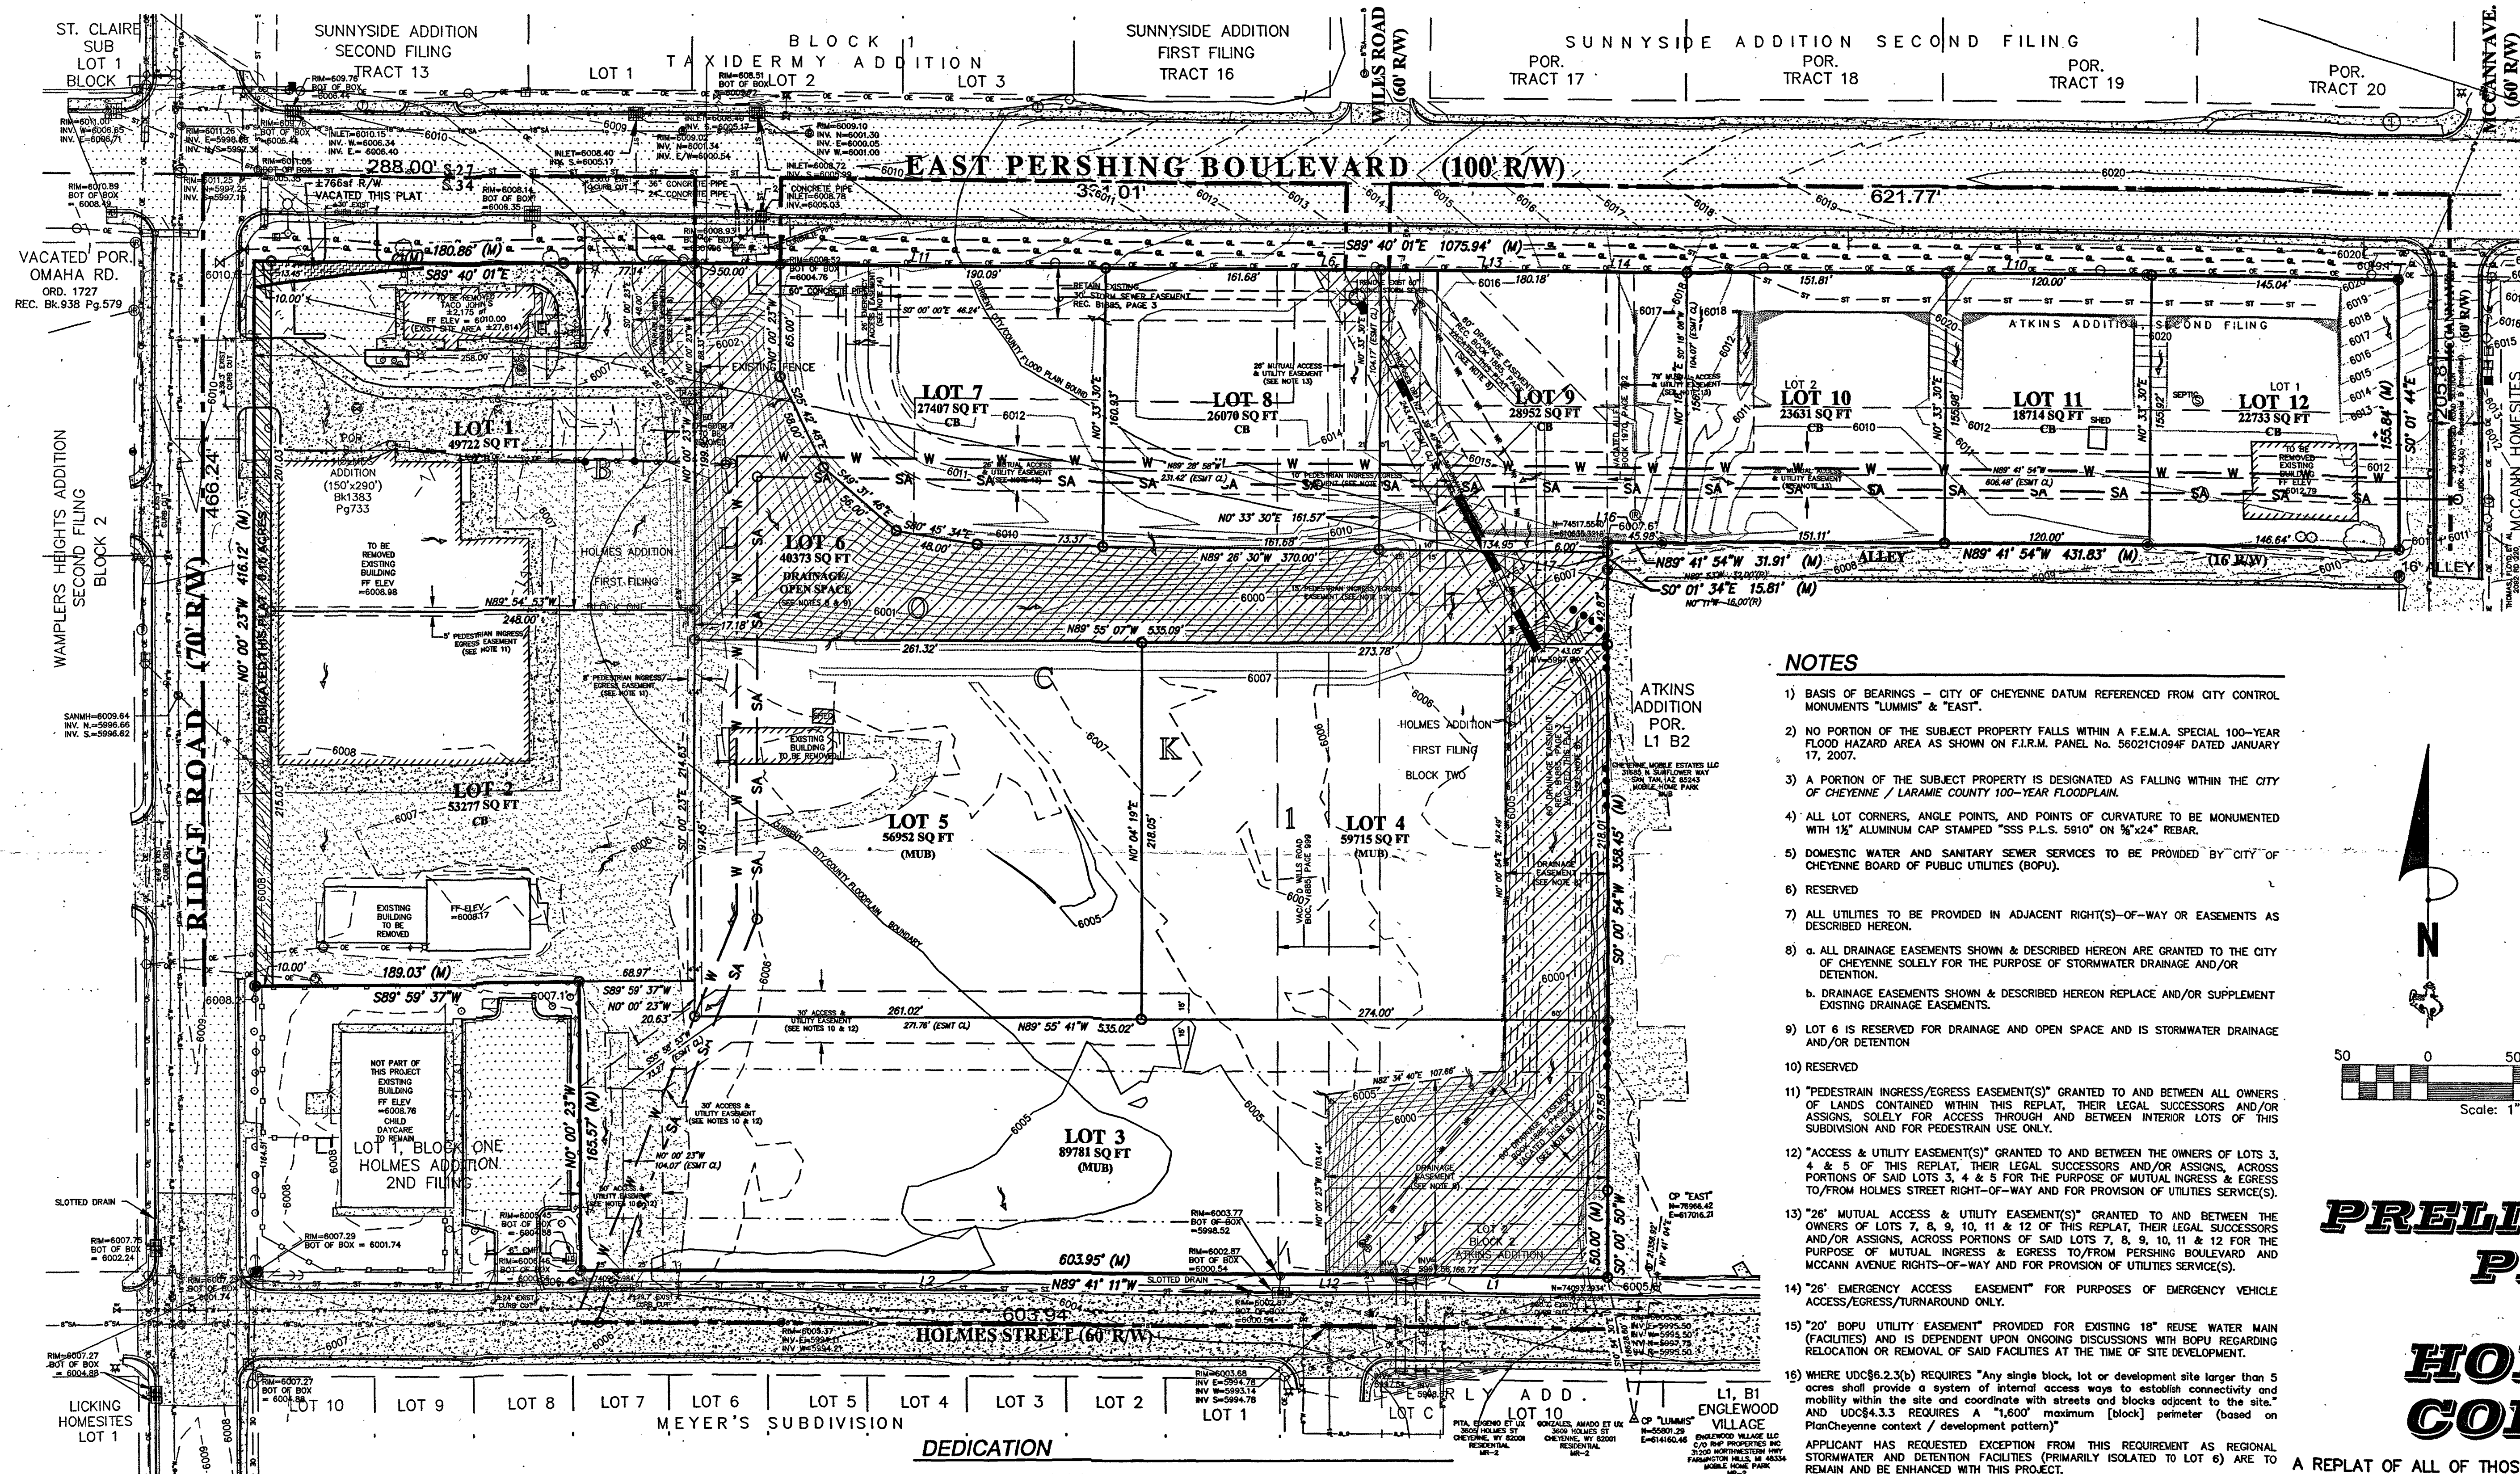

#### NOTES


- 1) BASIS OF BEARINGS - CITY OF CHEYENNE DATUM REFERENCED FROM CITY CONTROL MONUMENTS "LUMMIS" & "EAST".
- 2) NO PORTION OF THE SUBJECT PROPERTY FALLS WITHIN A F.E.M.A. SPECIAL 100-YEAR FLOOD HAZARD AREA AS SHOWN ON F.I.R.M. PANEL No. 56021C1094F DATED JANUARY 17, 2007.
- 3) A PORTION OF THE SUBJECT PROPERTY IS DESIGNATED AS FALLING WITHIN THE CITY OF CHEYENNE / LARAMIE COUNTY 100-YEAR FLOODPLAIN.
- 4) ALL LOT CORNERS, ANGLE POINTS, AND POINTS OF CURVATURE TO BE MONUMENTED WITH 1/2" ALUMINUM CAP STAMPED "SSS P.L.S. 5910" ON 3/4"x24" REBAR.
- 5) DOMESTIC WATER AND SANITARY SEWER SERVICES TO BE PROVIDED BY CITY OF CHEYENNE BOARD OF PUBLIC UTILITIES (BOPU).
- 6) RESERVED
- 7) ALL UTILITIES TO BE PROVIDED IN ADJACENT RIGHT(S)-OF-WAY OR EASEMENTS AS DESCRIBED HEREON.
- 8) a. ALL DRAINAGE EASEMENTS SHOWN & DESCRIBED HEREON ARE GRANTED TO THE CITY OF CHEYENNE SOLELY FOR THE PURPOSE OF STORMWATER DRAINAGE AND/OR DETENTION.  
b. DRAINAGE EASEMENTS SHOWN & DESCRIBED HEREON REPLACE AND/OR SUPPLEMENT EXISTING DRAINAGE EASEMENTS.
- 9) LOT 6 IS RESERVED FOR DRAINAGE AND OPEN SPACE AND IS STORMWATER DRAINAGE AND/OR DETENTION
- 10) RESERVED
- 11) "PEDESTRIAN INGRESS/EGRESS EASEMENT(S)" GRANTED TO AND BETWEEN ALL OWNERS OF LANDS CONTAINED WITHIN THIS REPLAT, THEIR LEGAL SUCCESSORS AND/OR ASSIGNS, SOLELY FOR ACCESS THROUGH AND BETWEEN INTERIOR LOTS OF THIS SUBDIVISION AND FOR PEDESTRIAN USE ONLY.
- 12) "ACCESS & UTILITY EASEMENT(S)" GRANTED TO AND BETWEEN THE OWNERS OF LOTS 3, 4 & 5 OF THIS REPLAT, THEIR LEGAL SUCCESSORS AND/OR ASSIGNS, ACROSS PORTIONS OF SAID LOTS 3, 4 & 5 FOR THE PURPOSE OF MUTUAL INGRESS & EGRESS TO/FROM HOLMES STREET RIGHT-OF-WAY AND FOR PROVISION OF UTILITIES SERVICE(S).
- 13) "26" MUTUAL ACCESS & UTILITY EASEMENT(S)" GRANTED TO AND BETWEEN THE OWNERS OF LOTS 7, 8, 9, 10, 11 & 12 OF THIS REPLAT, THEIR LEGAL SUCCESSORS AND/OR ASSIGNS, ACROSS PORTIONS OF SAID LOTS 7, 8, 9, 10, 11 & 12 FOR THE PURPOSE OF MUTUAL INGRESS & EGRESS TO/FROM PERSHING BOULEVARD AND MCCANN AVENUE RIGHTS-OF-WAY AND FOR PROVISION OF UTILITIES SERVICE(S).
- 14) "26" EMERGENCY ACCESS EASEMENT" FOR PURPOSES OF EMERGENCY VEHICLE ACCESS/EGRESS/TURNAROUND ONLY.
- 15) "20" BOPU UTILITY EASEMENT" PROVIDED FOR EXISTING 18" REUSE WATER MAIN (FACILITIES) AND IS DEPENDENT UPON ONGOING DISCUSSIONS WITH BOPU REGARDING RELOCATION OR REMOVAL OF SAID FACILITIES AT THE TIME OF SITE DEVELOPMENT.
- 16) WHERE UDC§6.2.3(b) REQUIRES "Any single block, lot or development site larger than 5 acres shall provide a system of internal access ways to establish connectivity and mobility within the site and coordinate with streets and blocks adjacent to the site." AND UDC§4.3.3 REQUIRES A "1,600' maximum [block] perimeter (based on PlanCheyenne context / development pattern)"  
APPLICANT HAS REQUESTED EXCEPTION FROM THIS REQUIREMENT AS REGIONAL STORMWATER AND DETENTION FACILITIES (PRIMARILY ISOLATED TO LOT 6) ARE TO REMAIN AND BE ENHANCED WITH THIS PROJECT.

## PRELIMINARY PLAT OF HOLMES CORNER

A REPLAT OF ALL OF THOSE REMAINING PORTIONS OF BLOCK ONE, HOLMES ADDITION, FIRST FILING; ALL OF BLOCK TWO, HOLMES ADDITION, FIRST FILING AND THAT PORTION OF VACATED WILLS ROAD WESTERLY OF AND ADJACENT THERETO; ALL OF LOT 1, BLOCK ONE, ATKINS ADDITION, SECOND FILING; ALL OF LOT 2, BLOCK ONE, ATKINS ADDITION, SECOND FILING AND THAT PORTION OF VACATED ALLEY WESTERLY OF AND ADJACENT THERETO; AND THAT ±766 SF PORTION OF PERSHING BOULEVARD AT THE SW CORNER OF THE INTERSECTION OF RIDGE ROAD AND PERSHING BOULEVARD;  
CITY OF CHEYENNE, LARAMIE COUNTY, WYOMING  
SITUATE IN THE NW¼ NW¼ OF SECTION 34,  
T.14N., R.66W., OF THE 6TH P.M.,  
LARAMIE COUNTY, WYOMING

PREPARED NOVEMBER, 2015

**STEEL SURVEYING SERVICES, LLC**  
PROFESSIONAL LAND SURVEYORS  
1102 WEST 19th ST. CHEYENNE, WY. 82001 • (307) 634-7273  
756 GILCHRIST ST. WHEATLAND, WY. 82201 • (307) 322-9789  
www.SteelSurvey.com • info@SteelSurvey.com

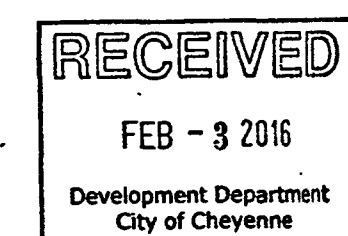

#### ZONING

EXISTING ZONE DISTRICT(S):  
±LOT 1 & LOT 2 : CB - COMMUNITY BUSINESS  
±LOTS 3 THRU 12 : MUB - MIXED-USE BUSINESS-EMPHASIS  
PROPOSED ZONE DISTRICT(S):  
LOT 1 & LOT 2 : EXISTING ZONING TO REMAIN  
LOTS 3 THRU 5 : EXISTING ZONING TO REMAIN  
LOTS 6 THRU 12 : CB - COMMUNITY BUSINESS

#### DEDICATION

KNOW ALL PERSONS BY THESE PRESENTS THAT: HWH ENTERPRISES LLC, a Wyoming Corporation, owner in fee simple of the following described lands:

All of those remaining portions of Block One, Holmes Addition, First Filing, AND All of Block Two, Holmes Addition, First Filing and that portion of vacated Wills Road westery of and adjacent thereto, AND All of Lot 1, Block One, Atkins Addition, AND All of Lot 2, Block One, Atkins Addition and that portion of vacated alley westery of and adjacent thereto, AND that ±766 sf portion of Pershing Boulevard at the SW corner of the intersection of Ridge Road and Pershing Boulevard; City of Cheyenne, Laramie County, Wyoming

Has caused the same to be surveyed, vacated, and re-platted to be known as HOLMES CORNER, and does hereby declare the subdivision of said land as it appears on this plat, to be their free act and deed and in accordance with their desires and do hereby grant the easements for the purposes indicated hereon.

HWH Enterprises, LLC, a Wyoming Corporation

by: \_\_\_\_\_ as \_\_\_\_\_

#### ENGINEER:

SUMMIT ENGINEERING  
5907 TOWNSEND PLACE  
CHEYENNE, WY 82009  
307-637-0681

#### OWNER:

HWH ENTERPRISES, LLC  
2800 OLIVE DR.  
CHEYENNE, WY 82001


#### SURVEYOR:

STEEL SURVEYING SERVICES, LLC  
1102 WEST 19th STREET  
CHEYENNE, WY 82001  
307-634-7273

#### DEVELOPER:

TBD

#### VICINITY MAP

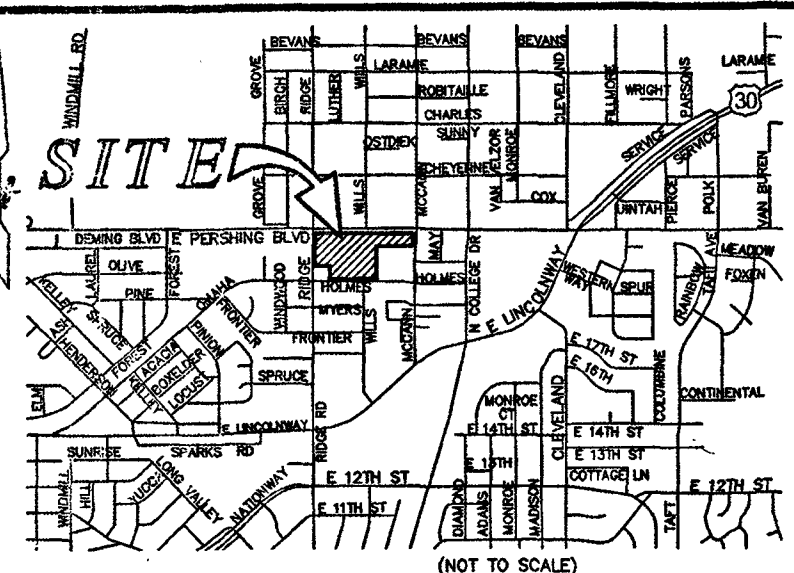

REVISED: February 2, 2016

\\2015 DWG\\15231 HWH HOLMES ADD REPLAT\\15231 REV FINAL PLAT.DWG