



Lummis/Read Annexation

Nathan Beauheim to: Seth Lloyd

06/09/2016 09:33 AM

Cc: Brandon Cammarata, Jack Studley, John Hall, "Rob Geringer",
Alessandra McCoy, Ben Rowland

History: This message has been forwarded.


Seth,

Here are Engineering's comments on including Campstool Road and the UPRR right-of-way in the Lummis/Read annexation:

1. The proposed Lummis/Read Annexation includes railroad and public road rights of way for the UPRR and Campstool Road. It is our understanding that a portion of the Campstool Road right of way is in the fee title ownership of the UPRR and was established under a lease arrangement for a County Road (Campstool Road). To the best of our knowledge, the lease has expired and is under renegotiation between the UPRR and Laramie County. In previous discussions with Laramie County, the City of Cheyenne had tentatively agreed to take maintenance responsibilities for Campstool Road once a new lease agreement had been established. However, no such documentation has been provided to the City of Cheyenne thus far to demonstrate that the issues surrounding this public road right of way had been resolved and a new lease established. With this in mind it would not be appropriate for the City of Cheyenne to take jurisdiction of this public road right of way without a clearly defined establishment of the road and conditions applicable. Excluding Campstool Road would not affect the contiguity of this proposed annexation as W.S.15-1-402(b) specifically provides for the exclusion of "... a public or private right of way, a public or private transportation right of way..." for contiguity purposes.
2. The proposed Lummis/Read Annexation would require further boundary survey to include the UPRR and Campstool Road rights of way Westward to the Original City of Cheyenne boundary. The cost and applicability of these survey requirements by this applicant do not appear to be justified.
3. The UPRR right of way further to the East has not been annexed, while areas to either side have been annexed. This demonstrating the precedence that UPRR right of way has not historically been annexed as a part of the adjacent area annexations. Annexing UPRR right of way could also put the City in violation of W.S.15-1-412 which requires the written consent of the landowner of any parcel or contiguous parcels in excess of 40 acres and \$40,000 in assessed valuation. UPRR appears to be a landowner meeting that threshold, especially if the additional area requested to be included by Laramie County is added.

CONCLUSION: Until such a time as proper documentation is provided to show a clearly defined establishment and continuing agreement with the UPRR for the Campstool Road (public road) right of way, the City of Cheyenne should not annex said road to the City. And to remain consistent, the railroad right of way should not be annexed unless consent is received from the UPRR to be a part thereof.

Nathan Beauheim, P.E.
Assistant City Engineer
City of Cheyenne
307-638-4315
Nbeauheim@cheyennecity.org

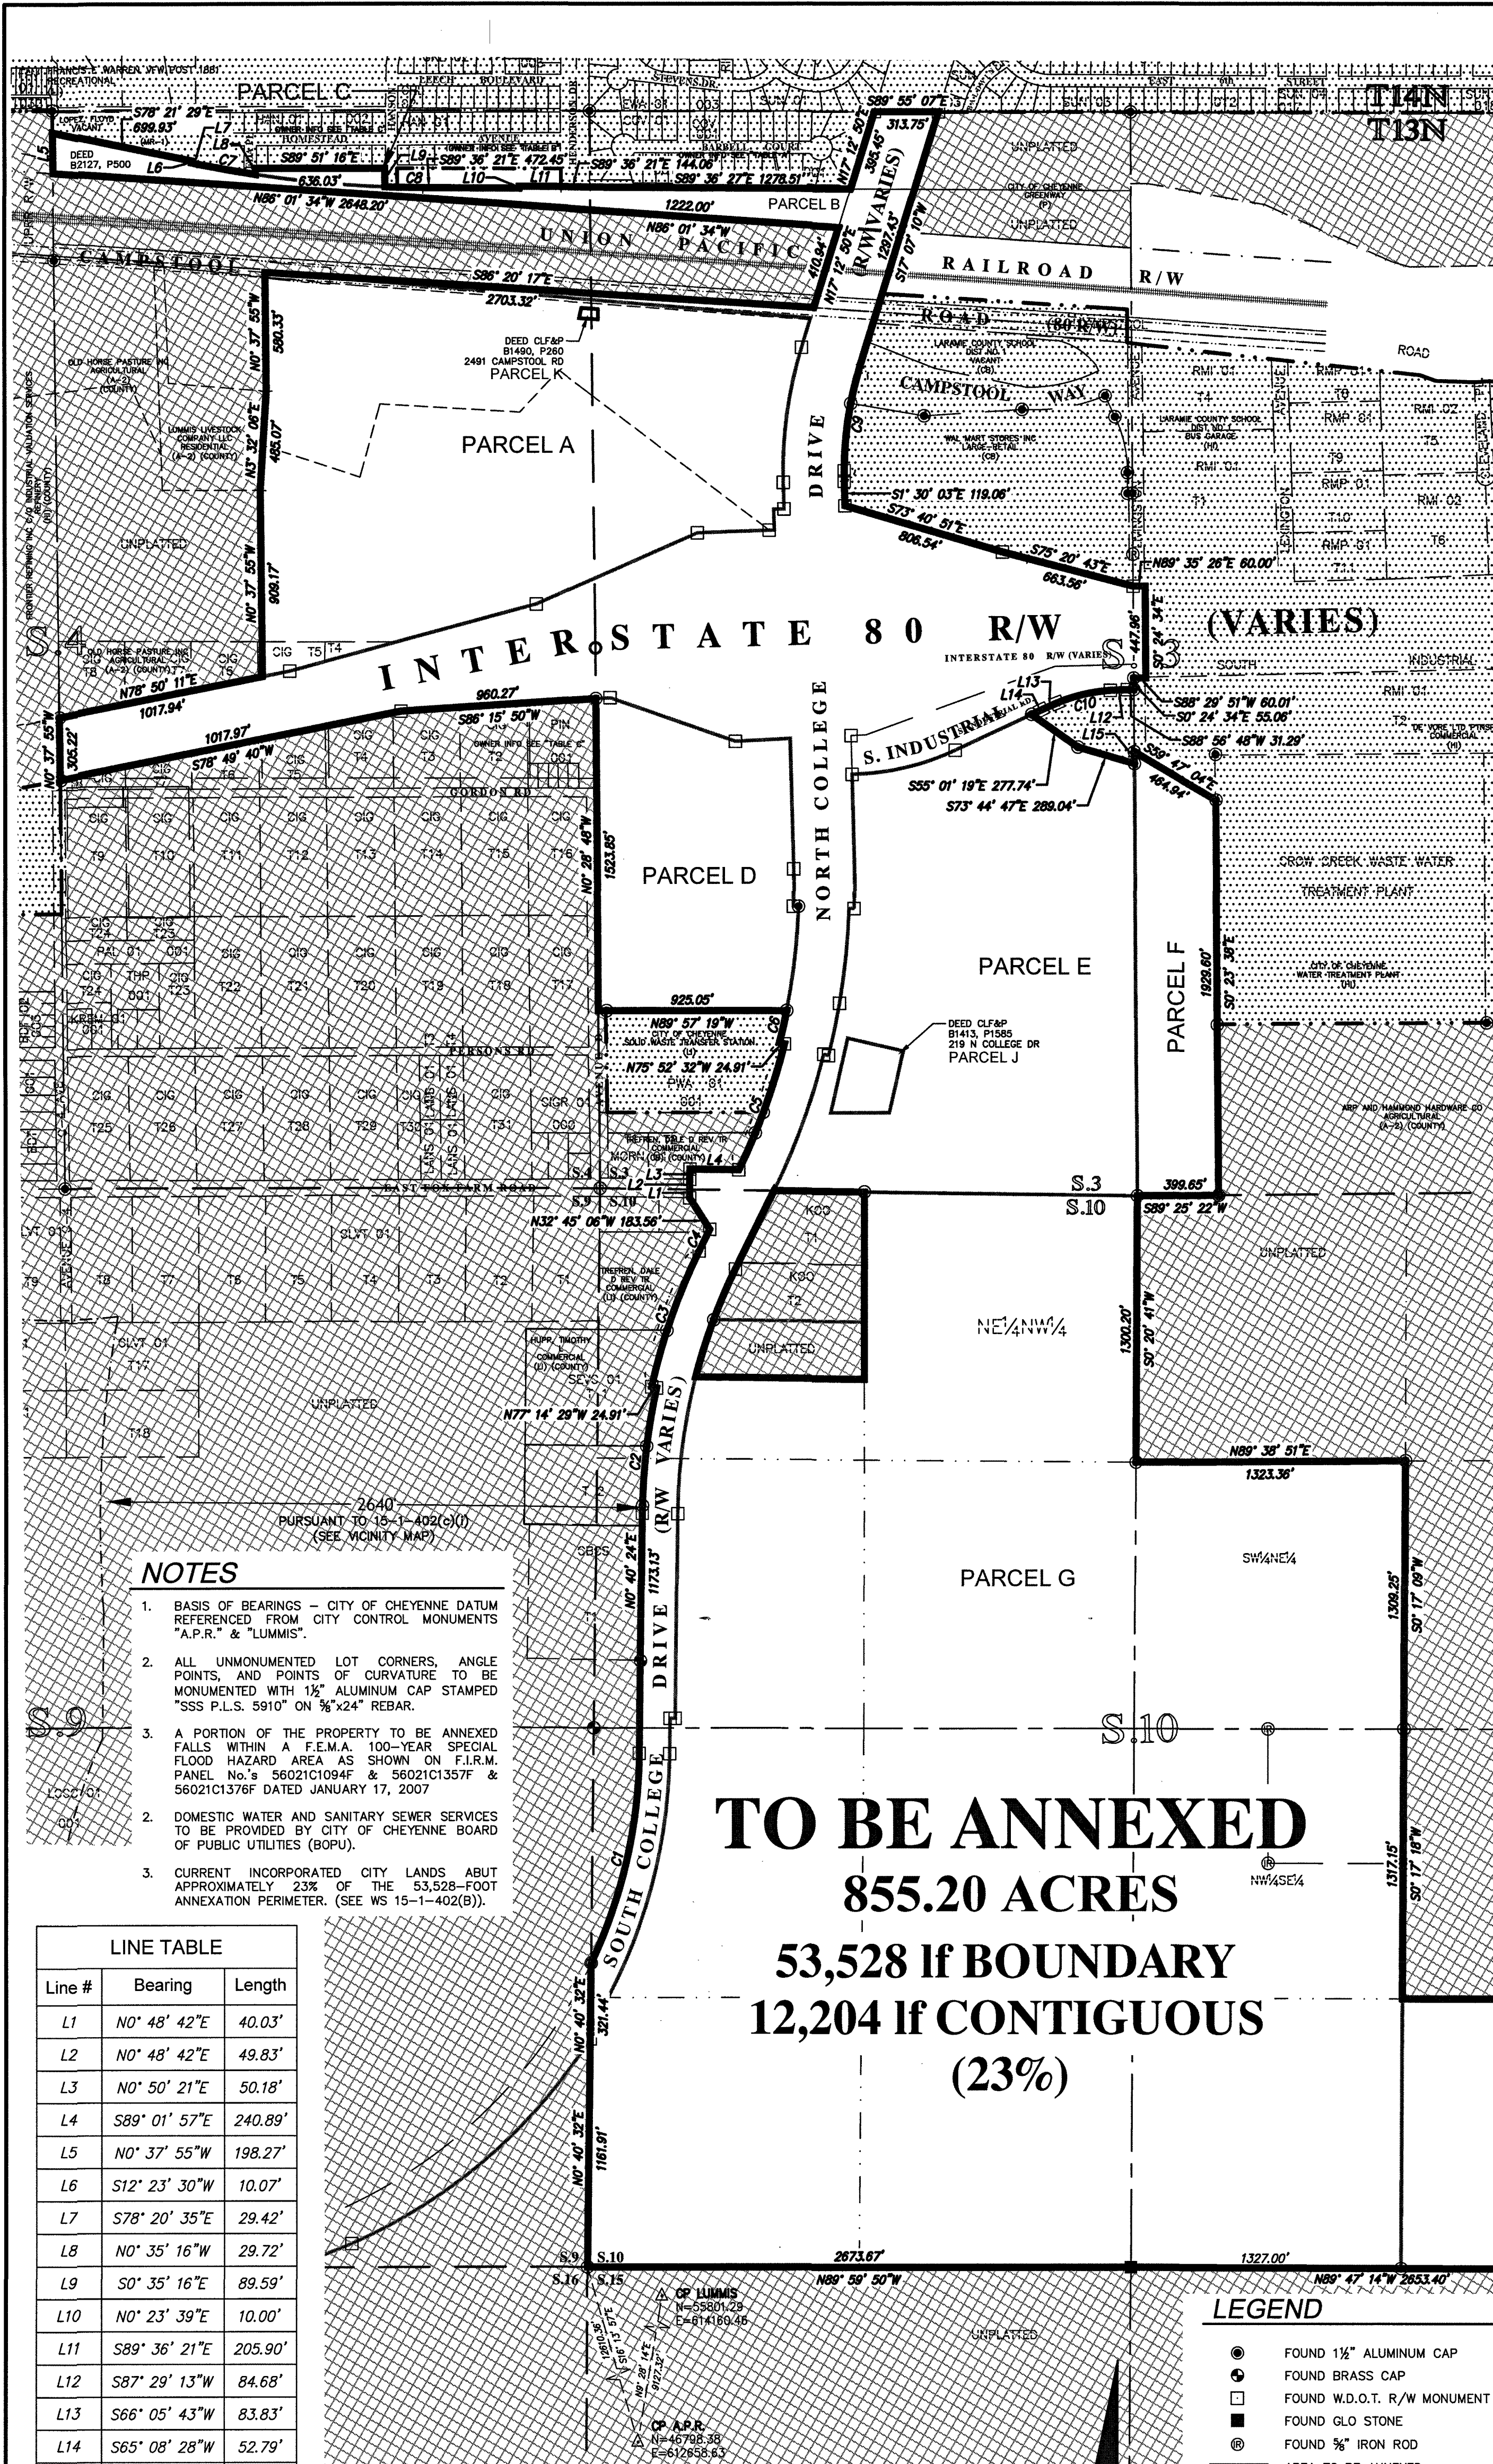

NOTES

1. BASIS OF BEARINGS - CITY OF CHEYENNE DATUM REFERENCED FROM CITY CONTROL MONUMENTS "A.P.R." & "LUMMIS".
2. ALL UNMONUMENTED LOT CORNERS, ANGLE POINTS, AND POINTS OF CURVATURE TO BE MONUMENTED WITH 1/2" ALUMINUM CAP STAMPED "SSS P.L.S. 5910" ON 3/4"x24" REBAR.
3. A PORTION OF THE PROPERTY TO BE ANNEXED FALLS WITHIN A FEMA 100-YEAR SPECIAL FLOOD HAZARD AREA AS SHOWN ON F.I.R.M. PANEL No. 5 56021C1094F & 56021C1357F & 56021C1376F DATED JANUARY 17, 2007
2. DOMESTIC WATER AND SANITARY SEWER SERVICES TO BE PROVIDED BY CITY OF CHEYENNE BOARD OF PUBLIC UTILITIES (BOPU).
3. CURRENT INCORPORATED CITY LANDS ABOUT APPROXIMATELY 23% OF THE 53,528-FOOT ANNEXATION PERIMETER. (SEE WS 15-1-402(B)).


LINE TABLE

Line #	Bearing	Length
L1	N0° 48' 42"E	40.03'
L2	N0° 48' 42"E	49.83'
L3	N0° 50' 21"E	50.18'
L4	S89° 01' 57"E	240.89'
L5	N0° 37' 55"W	198.27'
L6	S12° 23' 30"W	10.07'
L7	S78° 20' 35"E	29.42'
L8	N0° 35' 16"W	29.72'
L9	S0° 35' 16"E	89.59'
L10	N0° 23' 39"E	10.00'
L11	S89° 36' 21"E	205.90'
L12	S87° 29' 13"W	84.68'
L13	S66° 05' 43"W	83.83'
L14	S65° 08' 28"W	52.79'
L15	N0° 22' 25"W	56.95'

CURVE TABLE

CURVE #	DELTA	RADIUS	CHORD BEARING	CHORD LENGTH	ARC LENGTH
C1	24° 35' 18"	2471.48'	N13° 00' 48"E	1052.51'	1060.63'
C2	12° 00' 52"	2939.79'	N6° 40' 01"E	615.33'	616.46'
C3	13° 37' 36"	2964.79'	N19° 28' 18"E	703.46'	705.12'
C4	0° 10' 42"	37971.37'	N26° 22' 27"E	118.14'	118.14'
C5	11° 49' 04"	3174.10'	N20° 01' 01"E	653.52'	654.68'
C6	2° 54' 33"	3149.10'	N12° 39' 44"E	159.88'	159.89'
C7	2° 54' 42"	5679.65'	S79° 48' 01"E	288.60'	288.63'
C8	1° 53' 33"	5679.65'	S88° 39' 29"E	187.58'	187.59'
C9	18° 37' 33"	1761.20'	S7° 49' 12"W	570.01'	572.53'
C10	18° 06' 42"	854.94'	S76° 47' 28"W	269.13'	270.26'

VICINITY MAP

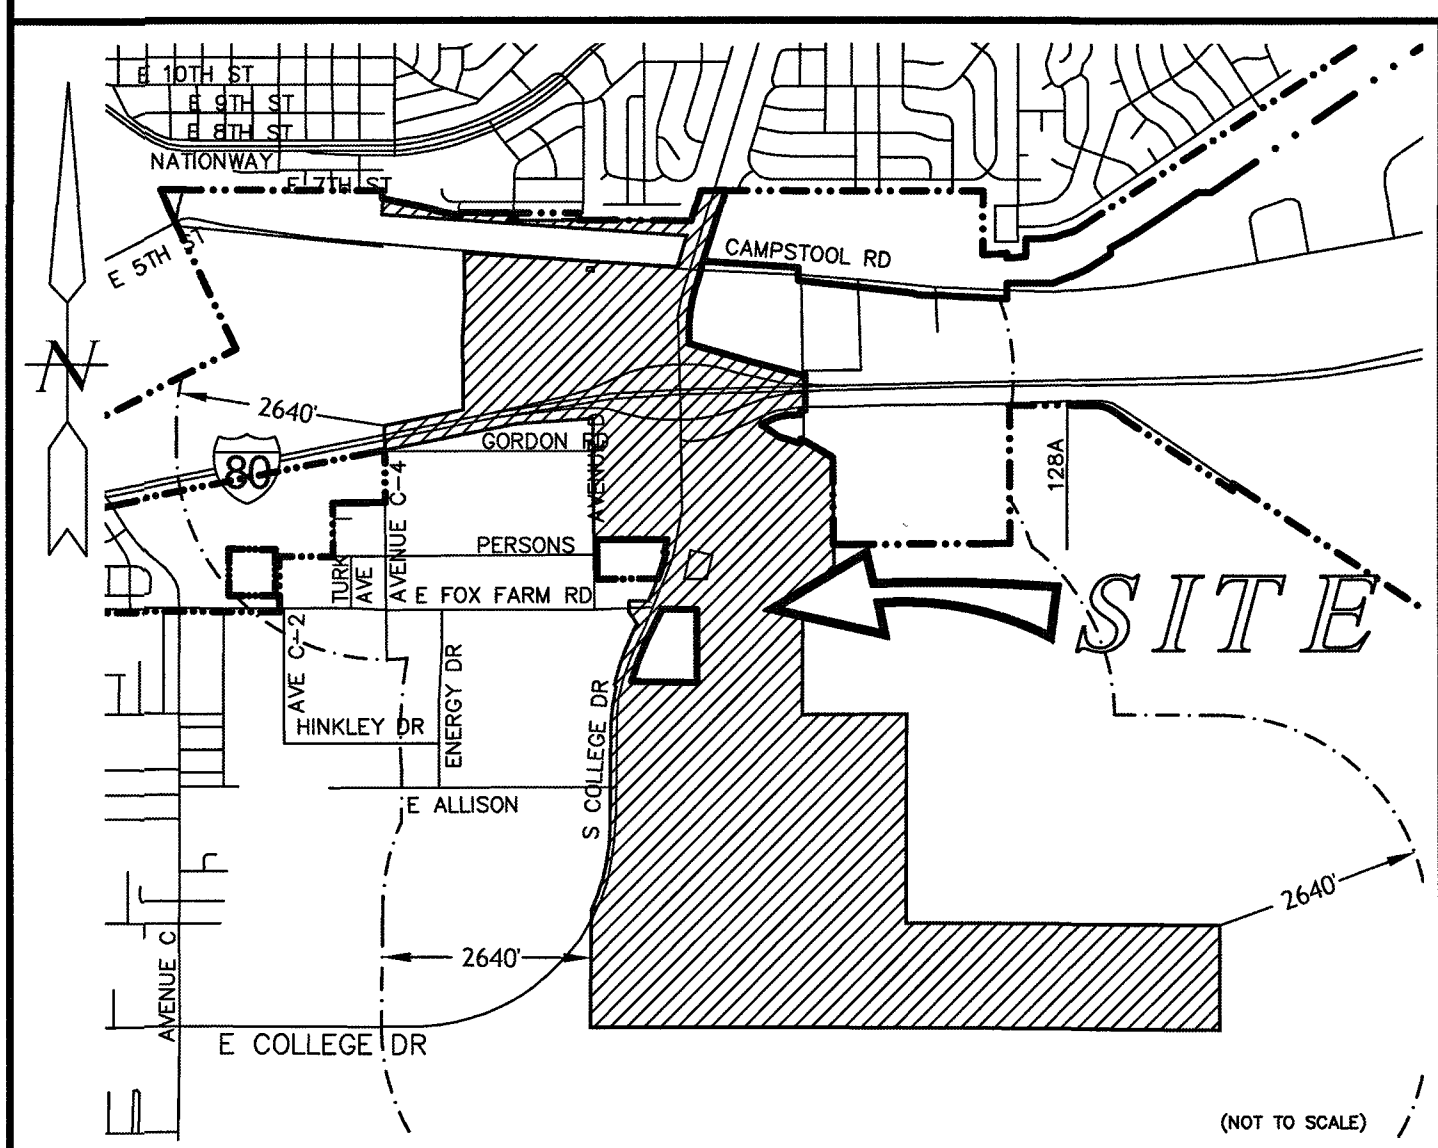

ADJACENT LANDOWNERS

TABLE A RESIDENTIAL (MR-1)	TABLE B VACANT (MR-1)
GLEASON, TIMOTHY ET UX CLOVER ADDITION: LOT 8	LANCASTER, BILL F ET UX CLOVER ADDITION: LOT 9
OLSEN, DANILLE ET VR CLOVER ADDITION: LOT 21	GREGORIO, WENDY M CLOVER ADDITION: LOT 11
FARLEY, DALE J CLOVER ADDITION: LOT 15	PHILLIPS, KRISTOPHER E ET UX CLOVER ADDITION: LOT 20
ERSEN, MICHAEL R ET UX CLOVER ADDITION: LOT 18	QUINCY, SCOTT R ET UX CLOVER ADDITION: LOT 16
PARRIS, THOMAS D ET UX CLOVER ADDITION: LOT 7	DELOREY, DANIEL F ET UX CLOVER ADDITION: LOT 23
HOGSEN, DOMINIC A CLOVER ADDITION: LOT 14	OSTER, JULIE A CLOVER ADDITION: LOT 13
POTTER, JASON ET UX CLOVER ADDITION: LOT 19	TROJANSKY, TIM EDWARD TR CLOVER ADDITION: LOT 17
CONNELL, KEVIN H CLOVER ADDITION: LOT 9	ADAMS, DOUGLAS G ET UX CLOVER ADDITION: LOT 22
DICAMILLO, DIANE ET UX CLOVER ADDITION: LOT 12	TABLE C RESIDENTIAL (MR-1)
RIEGER, DANIEL J ET UX CLOVER ADDITION: LOT 24	LAKLAND, KEITH ET UX HOMESTEAD ADDITION, 1ST FLUNG, REPLAT: LOT 8, BLOCK 4
	GUTIERREZ, FRANK ET UX JACOBY FLATS: TRACT 2
	MC HENRY, FRANK W ET UX CHEYENNE IRRIGATED GARDENS: POR OF TRACTS 6, 7 AND 8
	HAUGHT, KATHY JO ET AL CHEYENNE IRRIGATED GARDENS: SOUTH 440' OF TRACT 17
	GUTIERREZ, FRANK ET UX C/O ESPINOZA, MANUEL MARVIN ET UX JACOBY FLATS: TRACT 3
	WOLFE, ALBERT J ET UX HOMESTEAD ADDITION, 1ST FLUNG, REPLAT: LOT 3, BLOCK 4
	ALEXANDER, WILLIAM H D ET UX HOMESTEAD ADDITION, 1ST FLUNG, REPLAT: LOT 10, BLOCK 4
	RHODES, CHRISTINE S HOMESTEAD ADDITION, 1ST FLUNG, REPLAT: LOT 6, BLOCK 4
	LEONARD, MICHELLE S HOMESTEAD ADDITION, 1ST FLUNG, REPLAT: LOT 7, BLOCK 4
	TOTTENHOFF, CHERYL Y LUV TR HOMESTEAD ADDITION, 1ST FLUNG, REPLAT: LOT 1, BLOCK 4
	SANDERS, TIMOTHY J HOMESTEAD ADDITION, 1ST FLUNG, REPLAT: LOT 1, BLOCK 4
	BETTS, RONALD HOMESTEAD ADDITION, 1ST FLUNG, REPLAT: LOT 4, BLOCK 4
	YORK, EDDIE M REV TR ET AL YORK SUBDIVISION: LOT 1

TABLE D RESIDENTIAL (MR/COUNTY)	TABLE D (CONT.)
JACOBY, JOHN M JACOBY FLATS: TRACT 1	LEMONS, JOHN L CHEYENNE IRRIGATED GARDENS: POR TR 15 & 16
CLIFTON, NADAEAN M ET VR PINKNEY SUBDIVISION: LOT 6	RESIDENTIAL (PUD)
KEAVENY, JOHN T ET UX CHEYENNE IRRIGATED GARDENS: POR OF TRACTS 6, 7 AND 8	LEMONS, JOHN L ET UX CHEYENNE IRRIGATED GARDENS: POR TRACT 3
HAUGHT, KATHY JO ET AL CHEYENNE IRRIGATED GARDENS: SOUTH 440' OF TRACT 17	COMMERCIAL (UJ/COUNTY)
GUTIERREZ, FRANK ET UX C/O ESPINOZA, MANUEL MARVIN ET UX JACOBY FLATS: TRACT 3	STC CONSTRUCTION COA POR OF THE NE 1/4 SEC 9 SEVEN COUSINS SUBDIVISION: A POR OF TRACT 2
LEMONS, JOHN L CHEYENNE IRRIGATED GARDENS: POR OF TRACT 3	FERRO, RICK CLEAR VIEW TRACTS: TRACT 1, E 12' OF TRACT 2
FERRO, RICK CLEAR VIEW TRACTS: TRACT 1, E 12' OF TRACT 2	WYOMING BEARING AND SUPPLY LLC SEVEN COUSINS SUBDIVISION: A POR OF TRACT 2
FERRO, RICK CLEAR VIEW TRACTS: TRACT 1, E 12' OF TRACT 2	FERRO, RICK POR OF S1/2 NE 1/4 NE 1/4 SEC 9
FERRO, RICK CLEAR VIEW TRACTS: TRACT 1, E 12' OF TRACT 2	CONVERTER GROUP LLC SEVEN COUSINS SUBDIVISION: POR T 2
FERRO, RICK CLEAR VIEW TRACTS: TRACT 1, E 12' OF TRACT 2	ORELLI, REDD MIX INC CLEAR VIEW TRACTS: ALL OF TRACT 2
FERRO, RICK CLEAR VIEW TRACTS: TRACT 1, E 12' OF TRACT 2	CHURCH (PUD/COUNTY)
FERRO, RICK CLEAR VIEW TRACTS: TRACT 1, E 12' OF TRACT 2	LEMONS, JOHN L COMMUNITY COLLEGE FOUNDATION LOCAL ADDITION: LOT 1, BLOCK 1
FERRO, RICK CLEAR VIEW TRACTS: TRACT 1, E 12' OF TRACT 2	LEMONS, JOHN L COMMUNITY COLLEGE DISTRICT LOCAL ADDITION: POR LOT 1, BLOCK 1
FERRO, RICK CLEAR VIEW TRACTS: TRACT 1, E 12' OF TRACT 2	STATE OF WYOMING DEPT OF ADMIN AND INFO C/O COUNTY CORRECTION FACILITY C 8 SUBDIVISION: POR TRACT 1
FERRO, RICK CLEAR VIEW TRACTS: TRACT 1, E 12' OF TRACT 2	STATE OF WYOMING DEPT OF ADMIN AND INFO C 8 SUBDIVISION: A POR OF TRACT 1

FILING RECORD

TABLE D RESIDENTIAL (MR/COUNTY)	TABLE D (CONT.)
JACOBY, JOHN M JACOBY FLATS: TRACT 1	LEMONS, JOHN L CHEYENNE IRRIGATED GARDENS: POR TR 15 & 16
CLIFTON, NADAEAN M ET VR PINKNEY SUBDIVISION: LOT 6	RESIDENTIAL (PUD)
KEAVENY, JOHN T ET UX CHEYENNE IRRIGATED GARDENS: POR OF TRACTS 6, 7 AND 8	LEMONS, JOHN L ET UX CHEYENNE IRRIGATED GARDENS: POR TRACT 3
HAUGHT, KATHY JO ET AL CHEYENNE IRRIGATED GARDENS: SOUTH 440' OF TRACT 17	COMMERCIAL (UJ/COUNTY)
GUTIERREZ, FRANK ET UX C/O ESPINOZA, MANUEL MARVIN ET UX JACOBY FLATS: TRACT 3	STC CONSTRUCTION COA POR OF THE NE 1/4 SEC 9 SEVEN COUSINS SUBDIVISION: A POR OF TRACT 2
LEMONS, JOHN L CHEYENNE IRRIGATED GARDENS: POR OF TRACT 3	FERRO, RICK CLEAR VIEW TRACTS: TRACT 1, E 12' OF TRACT 2
FERRO, RICK CLEAR VIEW TRACTS: TRACT 1, E 12' OF TRACT 2	WYOMING BEARING AND SUPPLY LLC SEVEN COUSINS SUBDIVISION: A POR OF TRACT 2
FERRO, RICK CLEAR VIEW TRACTS: TRACT 1, E 12' OF TRACT 2	FERRO, RICK POR OF S1/2 NE 1/4 NE 1/4 SEC 9
FERRO, RICK CLEAR VIEW TRACTS: TRACT 1, E 12' OF TRACT 2	CONVERTER GROUP LLC SEVEN COUSINS SUBDIVISION: POR T 2
FERRO, RICK CLEAR VIEW TRACTS: TRACT 1, E 12' OF TRACT 2	ORELLI, REDD MIX INC CLEAR VIEW TRACTS: ALL OF TRACT 2
FERRO, RICK CLEAR VIEW TRACTS: TRACT 1, E 12' OF TRACT 2	CHURCH (PUD/COUNTY)
FERRO, RICK CLEAR VIEW TRACTS: TRACT 1, E 12' OF TRACT 2	LEMONS, JOHN L COMMUNITY COLLEGE FOUNDATION LOCAL ADDITION: LOT 1, BLOCK 1
FERRO, RICK CLEAR VIEW TRACTS: TRACT 1, E 12' OF TRACT 2	LEMONS, JOHN L COMMUNITY COLLEGE DISTRICT LOCAL ADDITION: POR LOT 1, BLOCK 1
FERRO, RICK CLEAR VIEW TRACTS: TRACT 1, E 12' OF TRACT 2	STATE OF WYOMING DEPT OF ADMIN AND INFO C/O COUNTY CORRECTION FACILITY C 8 SUBDIVISION: POR TRACT 1
FERRO, RICK CLEAR VIEW TRACTS: TRACT 1, E 12' OF TRACT 2	STATE OF WYOMING DEPT OF ADMIN AND INFO C 8 SUBDIVISION: A POR OF TRACT 1

LEGAL DESCRIPTION OF ANNEXATION BOUNDARY

A tract of land being a portion of Sections 3, 4, 10 and 11, Township 13 North, Range 66 West, 6th P.M., Laramie County, Wyoming, more particularly described as follows:

Beginning at the southwest corner of Section 10, thence N.00° 40' 32"E, along the west line of Section 10, a distance of 1181.91 feet to the south right-of-way of College Drive; thence N.00° 40' 32"E, a distance of 321.44 feet to the west right-of-way of College Drive; being beginning of a non-tangential curve to the left; thence along said right-of-way for the following 14 courses: thence 1060.63 feet along said curve, through an angle of 24° 35' 18", having a radius of 2471.48 feet, and whose long chord bears N 13° 00' 48"E, a distance of 1052.51 feet; thence N.00° 40' 24"E, a distance of 1173.13 feet to the beginning of a non-tangential curve to the right; thence 616.46 feet along said curve, through an angle of 12° 00' 52", having a radius of 2939.79 feet, and whose long chord bears N 06° 40' 01"E, a distance of 615.33 feet; thence N.77° 14' 29"W, a distance of 24.91 feet to the beginning of a non-tangential curve to the right; thence 705.12 feet along said curve, through 13° 37' 36", having a radius of 2964.79 feet, and whose long chord bears N 19° 28' 18"E, a distance of 703.46 feet to the beginning of a non-tangential curve to the right; thence 118.14 feet along said curve, through an angle of 0° 10' 42", having a radius of 37971.37 feet, and whose long chord bears N 26° 22' 27"E, a distance of 118.14 feet; thence N.32° 45' 06"W, a distance of 183.56 feet; thence N.00° 48' 42"E, a distance of 40.03 feet; thence N.00° 48' 42"E, a distance of 49.83 feet; thence N.00° 50' 21"E, a distance of 50.18 feet; thence S.89° 01' 57"E, a distance of 240.89 feet to the beginning of a non-tangential curve to the left; thence 654.68 feet along said curve, through an angle of 11° 49' 04", having a radius of 3174.10 feet, and whose long chord bears N 20° 01' 01"E, a distance of 653.52 feet to a point; thence N.75° 52' 32"W, a distance of 24.91 feet to the beginning of a non-tangential curve to the left; thence 159.89 feet along said curve, through an angle of 02° 54' 33", having a radius of 3149.10 feet, and whose long chord bears N 12° 39' 44"E, a distance of 159.88 feet; thence leaving said right-of-way, along the north line of Public Works Addition, N.89° 57' 19"W, a distance of 925.05 feet to the west line of Section 3; thence N.00° 28' 48"W, along said west line, a distance of 1523.85 feet to the south right-of-way of Interstate 80; thence S.86° 15' 50"W, along said right-of-way, a distance of 960.27 feet; thence S.78° 49' 40"W, along said right-of-way, a distance of 692.17 feet; thence S.78° 49' 40"W, along said right-of-way, a distance of 1017.97 feet to the west line of the East Half of Section 4; thence N.00° 39' 55"W, along said west line, (also being the west line of that remaining northerly portion of Tract 8, Cheyenne Irrigated Gardens), a distance of 305.22 feet to the north right-of-way of Interstate 80; thence N.78° 50' 11"E, along said right-of-way, a distance of 1017.94 feet; thence N.00° 37' 55"W, a distance of 909.17 feet; thence N.03° 32' 06"E, a distance of 485.07 feet; thence along said south line, S.86° 20' 17"E, a distance of 2703.32 feet to the west right-of-way line of College Drive; thence, along said west line, N.17° 12' 50"E, a distance of 410.94 feet to the south line of "Parcel 2", Book 2127, Page 500 Laramie County Clerk's Office; thence along said south dead line N.86° 01' 34"W, a distance of 1222.00 feet; thence continuing along said south dead line N.86° 01' 34"W, a distance of 2648.20 feet to the north-south centerline of Section 4; thence along north-south centerline (being the west line of said Parcel 2), N.00° 37' 55"W, a distance of 198.27 feet; to the northwest corner of said Parcel 2; thence along the west line, a distance of 1523.85 feet to the south right-of-way of Interstate 80; thence S.86° 15' 50"W, a distance of 960.27 feet; thence S.78° 49' 40"W, along said right-of-way, a distance of 692.17 feet; thence S.78° 49' 40"W, along said right-of-way, a distance of 1017.97 feet to the west line of the East Half of Section 4; thence N.00° 39' 55"W, along said west line, (also being the west line of that remaining northerly portion of Tract 8, Cheyenne Irrigated Gardens), a distance of 305.22 feet to the north right-of-way of Interstate 80; thence N.78° 50' 11"E, along said right-of-way, a distance of 1017.94 feet; thence N.00° 37' 55"W, a distance of 909.17 feet; thence N.03° 32' 06"E, a distance of 485.07 feet; thence along said south line, S.86° 20' 17"E, a distance of 2703.32 feet to the west right-of-way line of College Drive; thence, along said west line, N.17° 12' 50"E, a distance of 410.94 feet to the south line of "Parcel 2", Book 2127, Page 500 Laramie County Clerk's Office; thence along said south dead line N.86° 01' 34"W, a distance of 1222.00 feet; thence continuing along said south dead line N.86° 01' 34"W, a distance of 2648.20 feet to the north-south centerline of Section 4; thence along north-south centerline (being the west line of said Parcel 2), N.00° 37' 55"W, a distance of 198.27 feet; to the northwest corner of said Parcel 2; thence along the west line, a distance of 1523.85 feet to the south right-of-way of Interstate 80; thence S.86° 15' 50"W, a distance of 960.27 feet; thence S.78° 49' 40"W, along said right-of-way, a distance of 692.17 feet; thence S.78° 49' 40"W, along said right-of-way, a distance of 1017.97 feet to the west line of the East Half of Section 4; thence N.00° 39' 55"W, along said west line, (also being the west line of that remaining northerly portion of Tract 8, Cheyenne Irrigated Gardens), a distance of 305.22 feet to the north right-of-way of Interstate 80; thence N.78° 50' 11"E, along said right-of-way, a distance of 1017.94 feet; thence N.00° 37' 55"W, a distance of 909.17 feet; thence N.03° 32' 06"E, a distance of 485.07 feet; thence along said south line, S.86° 20' 17"E, a distance of 2703.32 feet to the west right-of-way line of College Drive; thence, along said west line, N.17° 12' 50"E, a distance of 410.94 feet to the south line of "Parcel 2", Book 2127, Page 500 Laramie County Clerk's Office; thence along said south dead line N.86° 01' 34"W, a distance of 1222.00 feet; thence continuing along said south dead line N.86° 01' 34"W, a distance of 2648.20 feet to the north-south centerline of Section 4; thence along north-south centerline (being the west line of said Parcel 2), N.00° 37' 55"W, a distance of 198.27 feet; to the northwest corner of said Parcel 2; thence along the west line, a distance of 1523.85 feet to the south right-of-way of Interstate 80; thence S.86° 15' 50"W, a distance of 960.27 feet; thence S.78° 49' 40"W, along said right-of-way, a distance of 692.17 feet; thence S.78° 49' 40"W, along said right-of-way, a distance of 1017.97 feet to the west line of the East Half of Section 4; thence N.00° 39' 55"W, along said west line, (also being the west line of that remaining northerly portion of Tract 8, Cheyenne Irrigated Gardens), a distance of 305.22 feet to the north right-of-way of Interstate 80; thence N.78° 50' 11"E, along said right-of-way, a distance of 1017.94 feet; thence N.00° 37' 55"W, a distance of 909.17 feet; thence N.03° 32' 06"E, a distance of 485.07 feet; thence along said south line, S.86° 20' 17"E, a distance of 2703.32 feet to the west right-of-way line of College Drive; thence, along said west line, N.17° 12' 50"E, a distance of 410.94 feet to the south line of "Parcel 2", Book 2127, Page 500 Laramie County Clerk's Office; thence along said south dead line N.86° 01' 34"W, a distance of 1222.00 feet; thence continuing along said south dead line N.86° 01' 34"W, a distance of 2648.20 feet to the north-south centerline of Section 4; thence along north-south centerline (being the west line of said Parcel 2), N.00° 37' 55"W, a distance of 198.27 feet; to the northwest corner of said Parcel 2; thence along the west line, a distance of 1523.85 feet to the south right-of-way of Interstate 80; thence S.86° 15' 50"W, a distance of 960.27 feet; thence S.78° 49' 40"W, along said right-of-way, a distance of 692.17 feet; thence S.78° 49' 40"W, along said right-of-way, a distance of 1017.97 feet to the west line of the East Half of Section 4; thence N.00° 39' 55"W, along said west line, (also being the west line of that remaining northerly portion of Tract 8, Cheyenne Irrigated Gardens), a distance of 305.22 feet to the north right-of-way of Interstate 80; thence N.78° 50' 11"E, along said right-of-way, a distance of 1017.94 feet; thence N.00° 37' 55"W, a distance of 909.17 feet; thence N.03° 32' 06"E, a distance of 485.07 feet; thence along said south line, S.86° 20' 17"E, a distance of 2703.32 feet to the west right-of-way line of College Drive; thence, along said west line, N.17° 12' 50"E, a distance of 410.94 feet to the south line of "Parcel 2", Book 2127, Page 500 Laramie County Clerk's Office; thence along said south dead line N.86° 01' 34"W, a distance of 1222.00 feet; thence continuing along said south dead line N.86° 01' 34"W, a distance of 2648.20 feet to the north-south centerline of Section 4; thence along north-south centerline (being the west line of said Parcel 2), N.00° 37' 55"W, a distance of 198.27 feet; to the northwest corner of said Parcel 2; thence along the west line, a distance of 1523.85 feet to the south right-of-way of Interstate 80; thence S.86° 15' 50"W, a distance of 960.27 feet; thence S.78° 49' 40"W, along said right-of-way, a distance of 692.17 feet; thence S.78° 49' 40"W, along said right-of-way, a distance of 1017.97 feet to the west line of the East Half of Section 4; thence N.00° 39' 55"W, along said west line, (also being the west line of that remaining northerly portion of Tract 8, Cheyenne Irrigated Gardens), a distance of 305.22 feet to the north right-of-way of Interstate 80; thence N.78° 50' 11"E, along said right-of-way, a distance of 1017.94 feet; thence N.00° 37' 55"W, a distance of 909.17 feet; thence N.03° 32' 06"E, a distance of 485.07 feet; thence along said south line, S.86° 20' 17"E, a distance of 2703.32 feet to the west right-of-way line of College Drive; thence, along said west line, N.17° 12' 50"E, a distance of 410.94 feet to the south line of "Parcel 2", Book 2127, Page 500 Laramie County Clerk's Office; thence along said south dead line N.86° 01' 34"W, a distance of 1222.00 feet; thence continuing along said south dead line N.86° 01' 34"W, a distance of 2648.20 feet to the north-south centerline of Section 4; thence along north-south centerline (being the west line of said Parcel 2), N.00° 37' 55"W, a distance of 198.27 feet; to the northwest corner of said Parcel 2; thence along the west line, a distance of 1523.85 feet to the south right-of-way of Interstate 80; thence S.86° 15' 50"W, a distance of 960.27 feet; thence S.78° 49' 40"W, along said right-of-way, a distance of 692.17 feet; thence S.78° 49' 40"W, along said right-of-way, a distance of 1017.97 feet to the west line of the East Half of Section 4; thence N.00° 39' 55"W, along said west line, (also being the west line of that remaining northerly portion of Tract 8, Cheyenne Irrigated Gardens), a distance of 305.22 feet to the north right-of-way of Interstate 80; thence N.78° 50' 11"E, along said right-of-way, a distance of 1017.94 feet; thence N.00° 37' 55"W, a distance of 909.17 feet; thence N.03° 32' 06"E, a distance of 485.07 feet; thence along said south line, S.86° 20' 17"E, a distance of 2703.32 feet to the west right-of-way line of College Drive; thence, along said west line, N.17° 12' 50"E, a distance of 410.94 feet to the south line of "Parcel 2", Book 2127, Page 500 Laramie County Clerk's Office; thence along said south dead line N.86° 01' 34"W, a distance of 1222.00 feet; thence continuing along said south dead line N.86° 01' 34"W, a distance of 2648.20 feet to the north-south centerline of Section 4; thence along north-south centerline (being the west line of said Parcel 2), N.00° 37' 55"W, a distance of 198.27 feet; to the northwest corner of said Parcel 2; thence along the west line, a distance of 1523.85 feet to the south right-of-way of Interstate 80; thence S.86° 15' 50"W, a distance of 960.27 feet; thence S.78° 49' 40"W, along said right-of-way, a distance of 692.17 feet; thence S.78° 49' 40"W, along said right-of-way, a distance of 1017.97 feet to the west line of the East Half of Section 4; thence N.00° 39' 55"W, along said west line, (also being the west line of that remaining northerly portion of Tract 8, Cheyenne Irrigated Gardens), a distance of 305.22 feet to the north right-of-way of Interstate 80; thence N.78° 50' 11"E, along said right-of-way, a distance of 1017.94 feet; thence N.00° 37' 55"W, a distance of 909.17 feet; thence N.03° 32' 06"E, a distance of 485.07 feet; thence along said south line, S.86° 20' 17"E, a distance of 2703.32 feet to the west right-of-way line of College Drive; thence, along said west line, N.17° 12' 50"E, a distance of 410.94 feet to the south line of "Parcel 2", Book 2127, Page 500 Laramie County Clerk's Office; thence along said south dead line N.86° 01' 34"W, a distance of 1222.00 feet; thence continuing along said south dead line N.86° 01' 34"W, a distance of 2648.20 feet to the north-south centerline of Section 4; thence along north-south centerline (being the west line of said Parcel 2), N.00° 37' 55"W, a distance of 198.27 feet; to the northwest corner of said Parcel 2; thence along the west line, a distance of 1523.85 feet to the south right-of-way of Interstate 80; thence S.86° 15' 50"W, a distance of 960.27 feet; thence S.78° 49' 40"W, along said right-of-way, a distance of 692.17 feet; thence S.78° 49' 40"W, along said right-of-way, a distance of 1017.97 feet to the west line of the East Half of Section 4; thence N.00° 39' 55"W, along said west line, (also being the west line of that remaining northerly portion of Tract 8, Cheyenne Irrigated Gardens), a distance of 305.22 feet to the north right-of-way of Interstate 80; thence N.78° 50' 11"E, along said right-of-way, a distance of 1017.94 feet; thence N.00° 37' 55"W, a distance of 909.17 feet; thence N.03° 32' 06"E, a distance of 485.07 feet; thence along said south line, S.86° 20' 17"E, a distance of 2703.32 feet to the west right-of-way line of College Drive; thence, along said west line, N.17° 12' 50"E, a distance of 410.94 feet to the south line of "Parcel 2", Book 2127, Page 500 Laramie County Clerk's Office; thence along said south dead line N.86° 01' 34"W, a distance of 1222.00 feet; thence continuing along said south dead line N.86° 01' 34"W, a distance of 2648.20 feet to the north-south centerline of Section 4; thence along north-south centerline (being the west line of said Parcel 2), N.00° 37' 55"W, a distance of 198.27 feet; to the northwest corner of said Parcel 2; thence along the west line, a distance of 1523.85 feet to the south right-of-way of Interstate 80; thence S.86° 15' 50"W, a distance of 960.27 feet; thence S.78° 49' 40"W, along said right-of-way, a distance of 692.17 feet; thence S.78° 49' 40"W, along said right-of-way, a distance of 1017.97 feet to the west line of the East Half of Section 4; thence N.00° 39' 55"W, along said west line, (also being the west line of that remaining northerly portion of Tract 8, Cheyenne Irrigated Gardens), a distance of 305.22 feet to the north right-of-way of Interstate 80; thence N.78° 50' 11"E, along said right-of-way, a distance of 1017.94 feet; thence N.00° 37' 55"W, a distance of 909.17 feet; thence N.03° 32' 06"E, a distance of 485.07 feet; thence along said south line, S.86° 20' 17"E, a distance of 2703.32 feet to the west right-of-way line of College Drive; thence, along said west line, N.17° 12' 50"E, a distance of 410.94 feet to the south line of "Parcel 2", Book 2127, Page 500 Laramie County Clerk's Office; thence along said south dead line N.86° 01' 34"W, a distance of 1222.00 feet; thence continuing along said south dead line N.86° 01' 34"W, a distance of 2648.20 feet to the north-south centerline of Section 4; thence along north-south centerline (being the west line of said Parcel 2), N.00° 37' 55"W, a distance of 198.27 feet; to the northwest corner of said Parcel 2; thence along the west line, a distance of 1523.85 feet to the south right-of-way of Interstate 80; thence S.86° 15' 50"W, a distance of 960.27 feet; thence S.78° 49' 40"W, along said right-of-way, a distance of 692.17 feet; thence S.78° 49' 40"W, along said right-of-way, a distance of 1017.97 feet to the west line of the East Half of Section 4; thence N.00° 39' 55"W, along said west line, (also being the west line of that remaining northerly portion of Tract 8, Cheyenne Irrigated Gardens), a distance of 305.22 feet to the north right-of-way of Interstate 80; thence N.78° 50' 11"E, along said right-of-way, a distance of 1017.94 feet; thence N.00° 37' 55"W, a distance of 909.17 feet; thence N.03° 32' 06"E, a distance of 485.07 feet; thence along said south line, S.86° 20' 17"E, a distance of 2703.32 feet to the west right-of-way line of College Drive; thence, along said west line, N.17° 12'